CUSTOM CASEWORK · REQUEST FOR QUOTATION

LC-60 laptop storage cabinet


Sixty laptops in twelve bays of five behind two lockable doors. 49" wide, 19" deep with doors, 35" tall. 1" panels throughout, 4" toe-kick base.

DESIGN BASIS

Laptop footprint	10" x 14", 1-1/2" thick
Stack limit	5 laptops = 7-1/2" tall
Capacity	60 laptops = 12 stacks (required 60)
Layout	4 columns x 3 tiers = 12 bays
Clear bay	11" W x 9" H x 17-1/2" D
Clearance per stack	1/2" each side, 1-1/2" above, 3" in front, 1/2" behind
Overall size	49" W x 19" D x 35" H (18" carcass + 1" doors)
Doors	2, each over 2 columns, hinged on the center divider, keyed alike
Panels	1" sides, top, deck, shelves, dividers, doors. 1/2" back
Base	4" toe kick, recessed 3"; first bay floor at 5"
Weight (approx.)	233 lb empty, 533 lb loaded at 5 lb per laptop

GENERAL NOTES

1. All dimensions are finished sizes in inches. Overall height is floor to top of top, glides at minimum.
2. Board: 1" industrial particleboard, 45 lb density minimum, thermally fused laminate both faces. Back: 1/2" MDF, TFM both faces. Color by owner, to be confirmed.
3. Edgeband: 3 mm PVC on every exposed edge, color-matched. See cut list A-401.
4. Joinery: 8 mm dowels plus confirmat screws, factory assembled. Knock-down cam fittings acceptable if stated in the quote.
5. Shelves are fixed and carried by dividers every 12". Minimum 50 lb per bay.
6. Laptops sit 1/2" from the back panel, leaving 3" in front of each stack behind the door.
7. Glides add about 3/8". If 35" is a hard maximum, cut toe kick, rear rail and notch to 3-5/8".
8. Anchor to the wall with the anti-tip kit (H06). Loaded weight is about 533 lb.
9. Confirm laptop size against an owner sample before cutting.

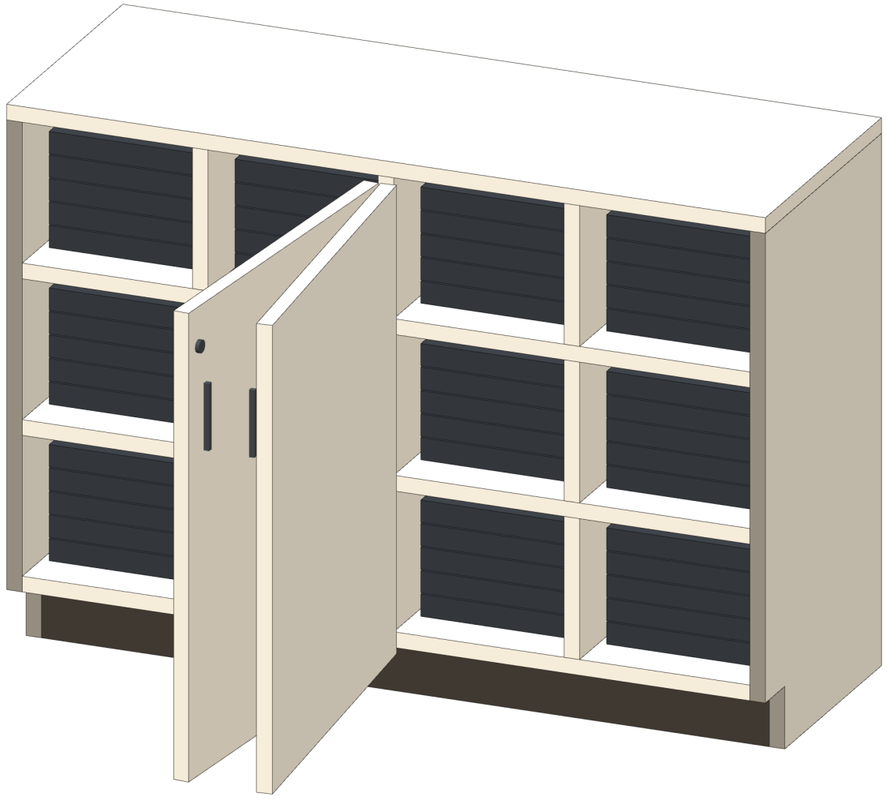

ISOMETRIC · DOORS OPEN, LOADED WITH 60 LAPTOPS

SHEET INDEX

A-001	Cover, design basis, notes	A-202	Exploded isometric
A-101	Front elevation, doors closed	A-301	Part details 1
A-102	Interior elevation, doors removed	A-302	Part details 2
A-103	Section A-A, side elevation, bay	A-303	Door details
A-104	Top plan, plan section B-B	A-401	Cut list and hardware
A-105	Interior elevation, loaded	A-501	Alternates, quote request
A-201	Isometric views		

OF4S

Office Furniture 4 Sale
1790 W 8th Ave, Hialeah, FL 33010
+1 305 889 3364 · officefurniture4sale.com

PROJECT
LC-60 laptop storage cabinet

CLIENT
To be confirmed

DRAWING
Cover, design basis, notes

SCALE
As noted

DATE
Nov 9, 2026

REVISION
2 · Two doors, center hinged

UNITS
Inches. Use written dimensions; do not scale.

STATUS
For quotation. Fabricator submits shop drawings and finish samples for approval before production.


REV · DATE · DESCRIPTION

0 · 11/04/26 · Issued for pricing
1 · 11/04/26 · Doors in base scope; depth 16" to 18"; stacks to rear
2 · 11/09/26 · Two doors, both hinged on center divider, swing outward

SHEET
A-001

ELEVATIONS

Front elevation, doors closed

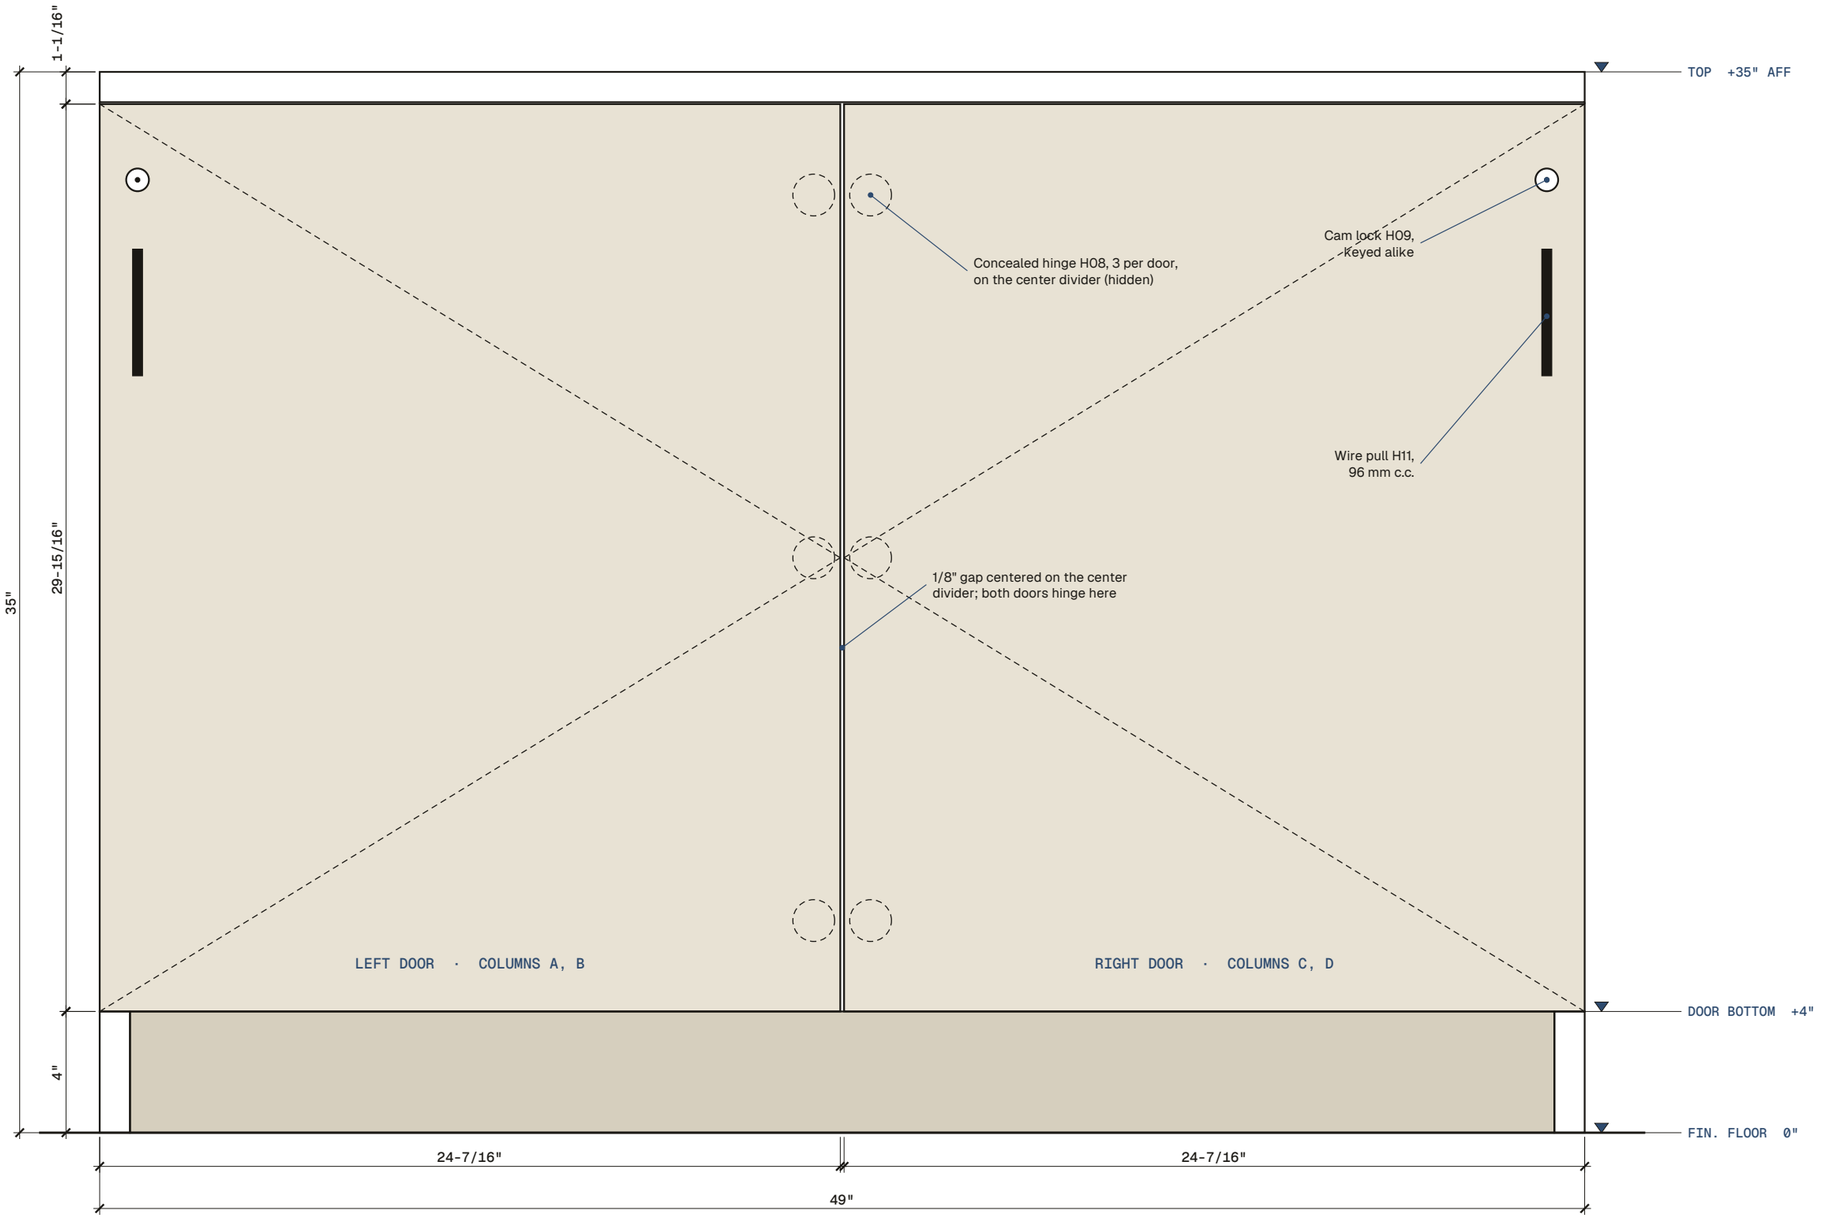

1 **Front elevation, doors closed**

SCALE 1:5

OF4S

Office Furniture 4 Sale
1790 W 8th Ave, Hialeah, FL 33010
+1 305 889 3364 · officefurniture4sale.com

PROJECT
LC-60 laptop storage cabinet

CLIENT
To be confirmed

DRAWING
Front elevation, doors closed

SCALE
1:5 at 11 x 17

DATE
Nov 9, 2026

REVISION
2 · Two doors, center hinged

UNITS
Inches. Use written dimensions; do not scale.

STATUS
For quotation. Fabricator submits shop drawings and finish samples for approval before production.


REV · DATE · DESCRIPTION

0 · 11/04/26 · Issued for pricing
1 · 11/04/26 · Doors in base scope; depth 16" to 18"; stacks to rear
2 · 11/09/26 · Two doors, both hinged on center divider, swing outward

SHEET
A-101

ELEVATIONS

Interior elevation, doors removed

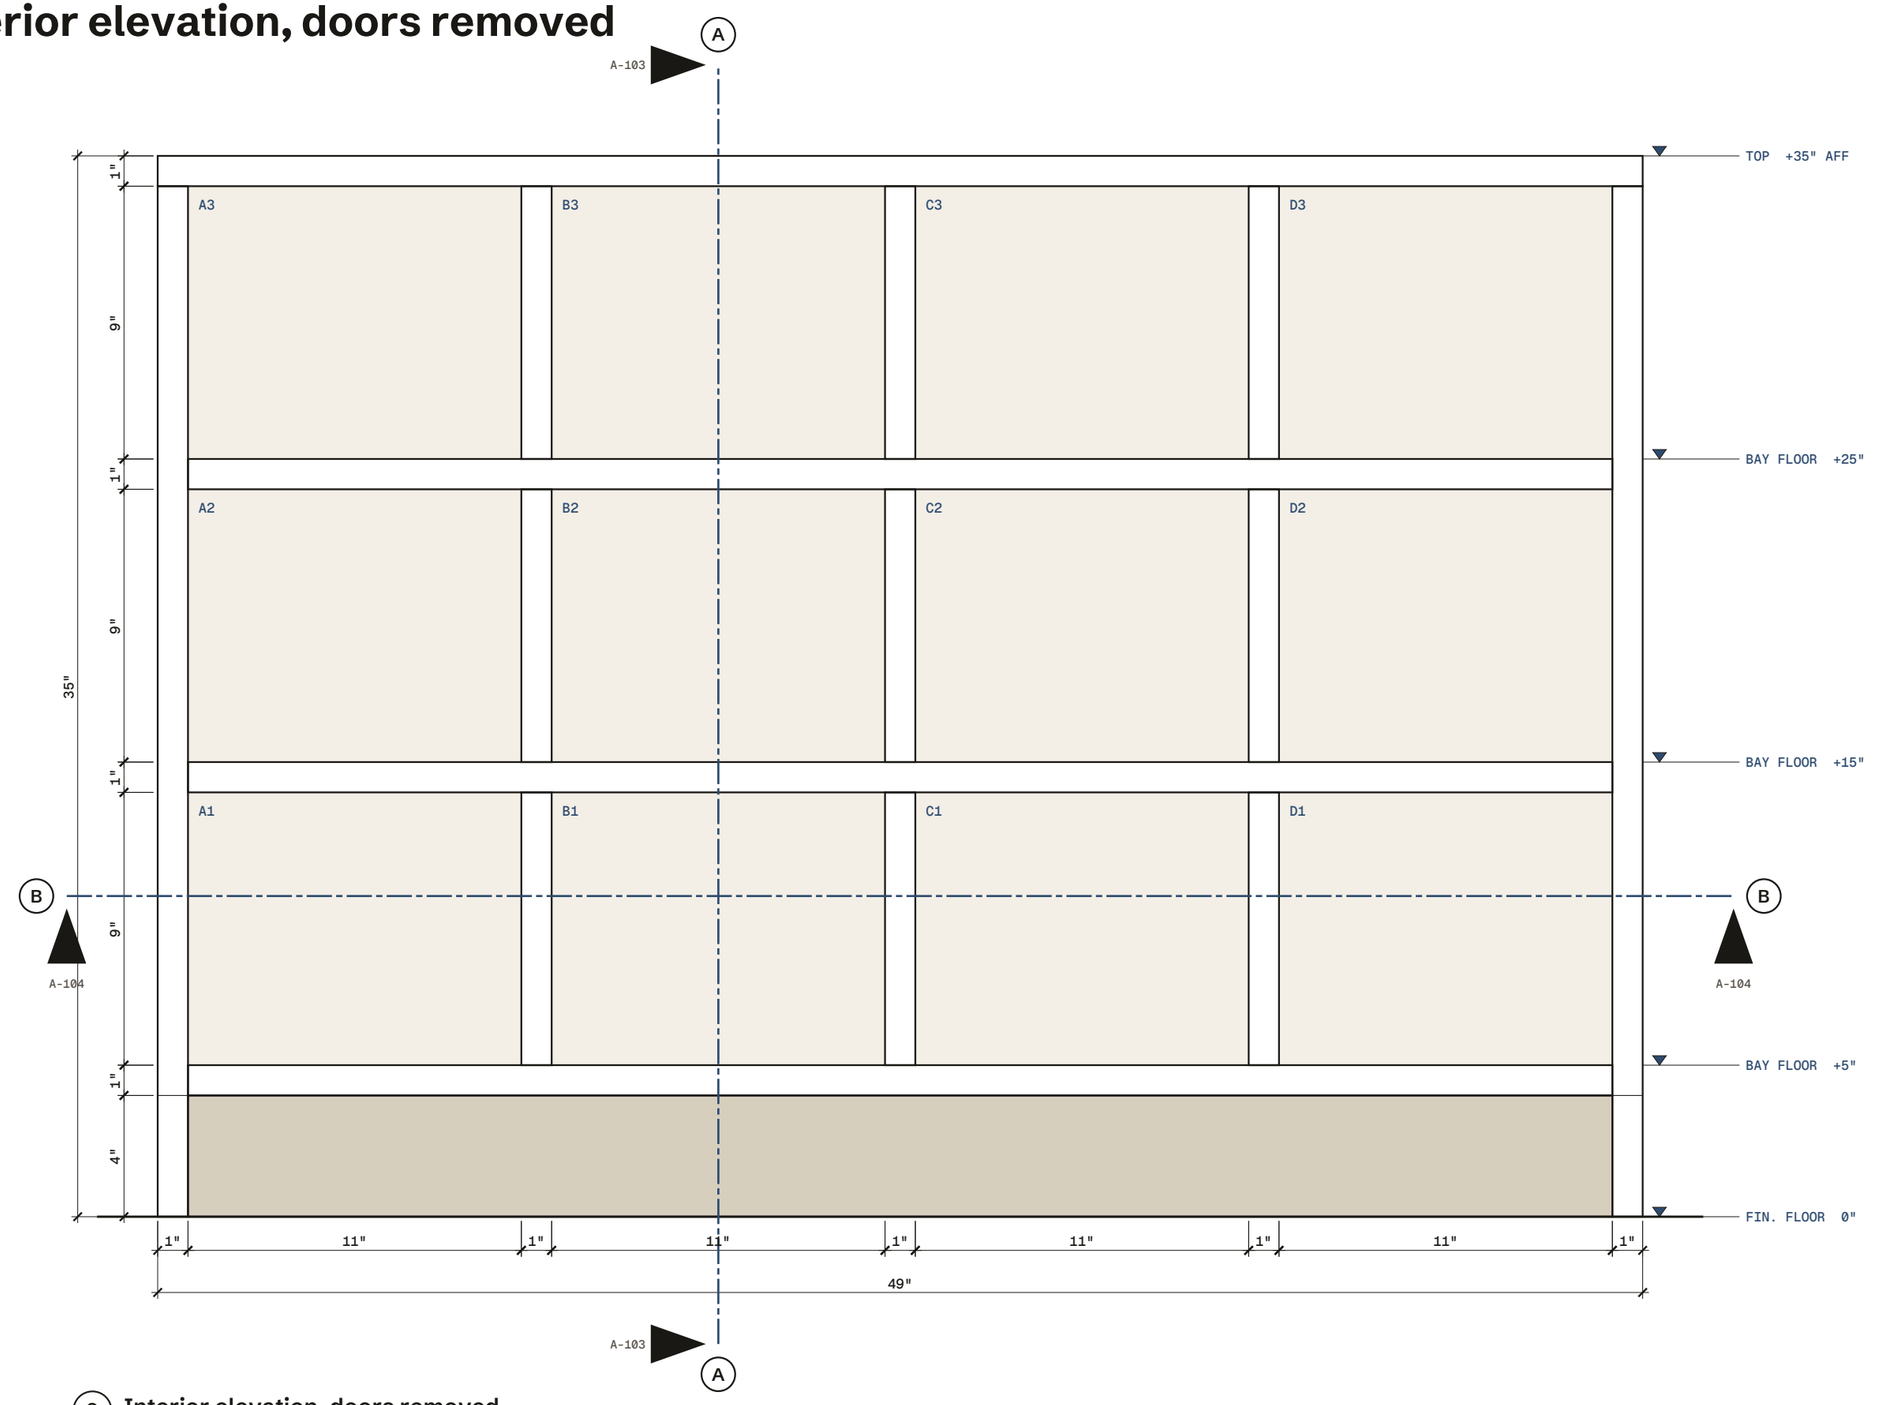

2 **Interior elevation, doors removed**

SCALE 1:5 · DOORS ON A-101

OF4S

Office Furniture 4 Sale
1790 W 8th Ave, Hialeah, FL 33010
+1 305 889 3364 · officefurniture4sale.com

PROJECT
LC-60 laptop storage cabinet

CLIENT
To be confirmed

DRAWING
Interior elevation, doors removed

SCALE
1:5 at 11 x 17

DATE
Nov 9, 2026

REVISION
2 · Two doors, center hinged

UNITS
Inches. Use written dimensions; do not scale.

STATUS
For quotation. Fabricator submits shop drawings and finish samples for approval before production.


REV · DATE · DESCRIPTION

0 · 11/04/26 · Issued for pricing
1 · 11/04/26 · Doors in base scope; depth 16" to 18"; stacks to rear
2 · 11/09/26 · Two doors, both hinged on center divider, swing outward

SHEET
A-102


SECTIONS AND DETAILS

Section A-A, side elevation, bay detail

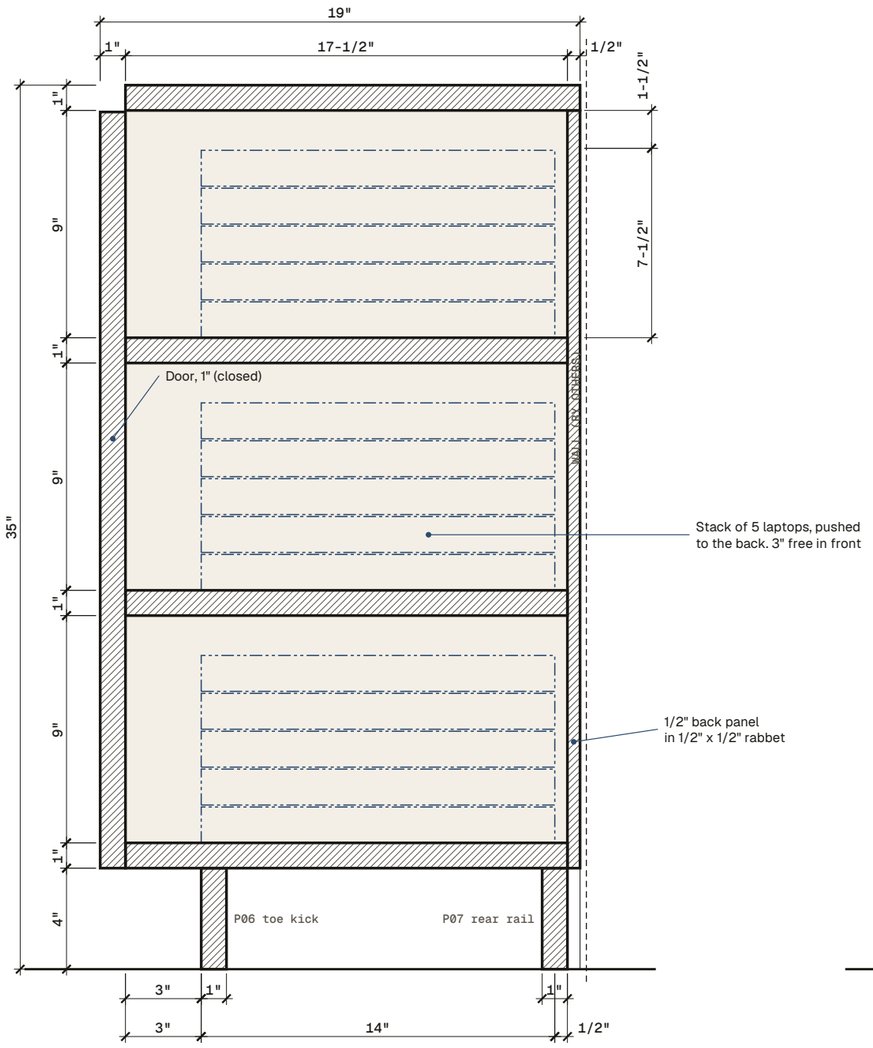


3 **Section A-A**

SCALE 1:6 · SEE A-102

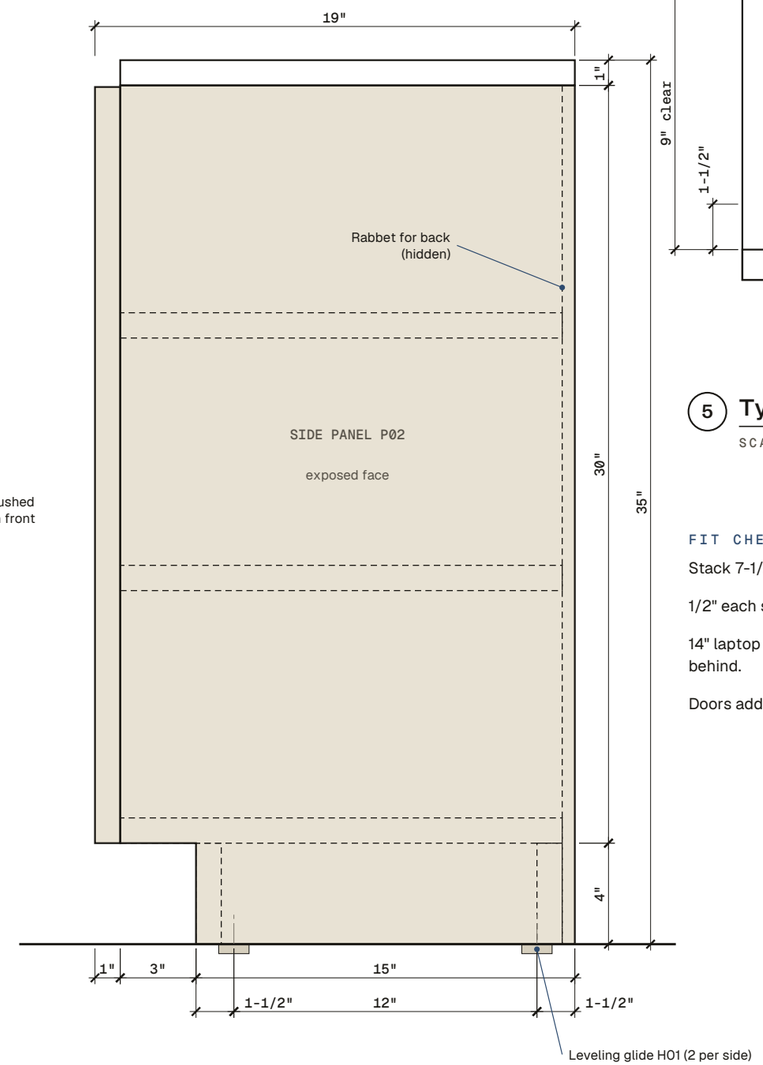

4 **Right side elevation**

SCALE 1:6 · LEFT SIDE MIRROR

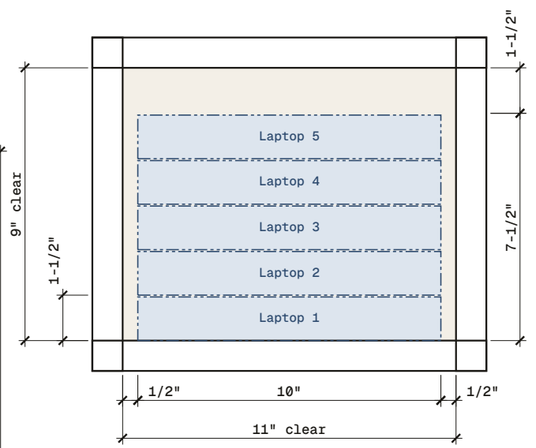

5 **Typical bay**

SCALE 1:5

FIT CHECK

Stack 7-1/2" in a 9" bay leaves 1-1/2" to lift the top laptop.

1/2" each side for fingers and rubber feet.

14" laptop in 17-1/2" depth, pushed back: 3" in front, 1/2" behind.

Doors add 1": 19" overall depth.

OF4S

Office Furniture 4 Sale
1790 W 8th Ave, Hialeah, FL 33010
+1 305 889 3364 · officefurniture4sale.com

PROJECT
LC-60 laptop storage cabinet

CLIENT
To be confirmed

DRAWING
Section A-A, side elevation, bay

SCALE
1:6, 1:5 at 11 x 17

DATE
Nov 9, 2026

REVISION
2 · Two doors, center hinged

UNITS
Inches. Use written dimensions; do not scale.

STATUS
For quotation. Fabricator submits shop drawings and finish samples for approval before production.


REV · DATE · DESCRIPTION

0 · 11/04/26 · Issued for pricing
1 · 11/04/26 · Doors in base scope; depth 16" to 18"; stacks to rear
2 · 11/09/26 · Two doors, both hinged on center divider, swing outward

SHEET
A-103


PLANS

Top plan and plan section B-B

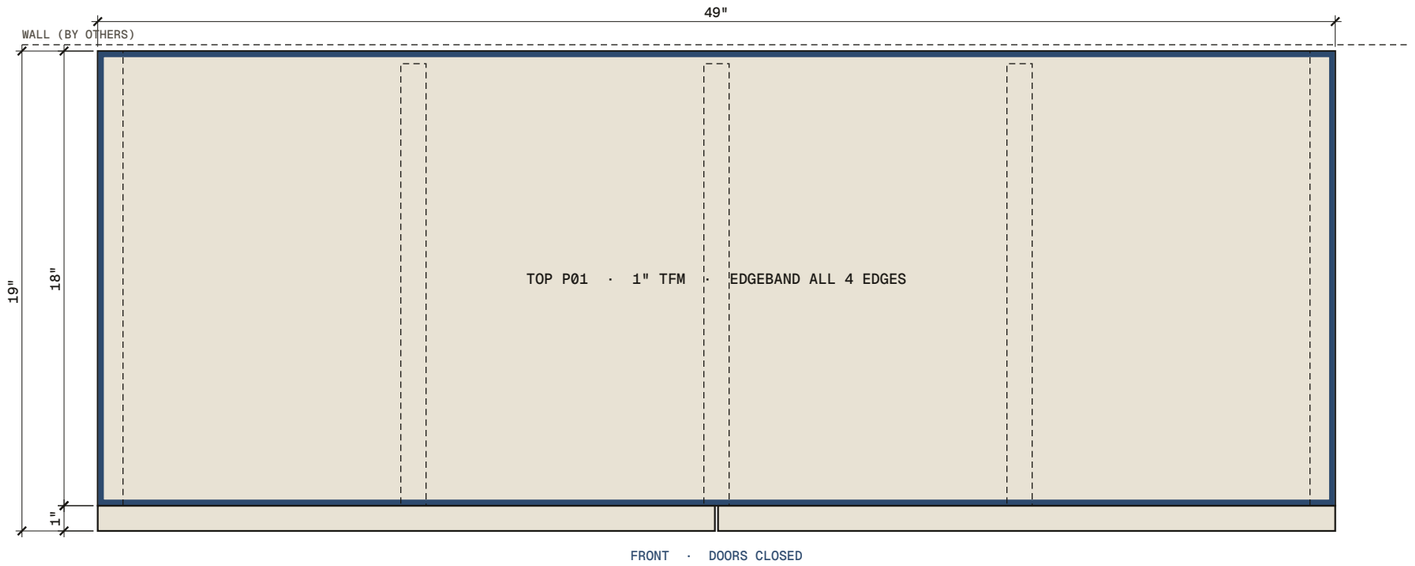

6 Top plan

SCALE 1:6

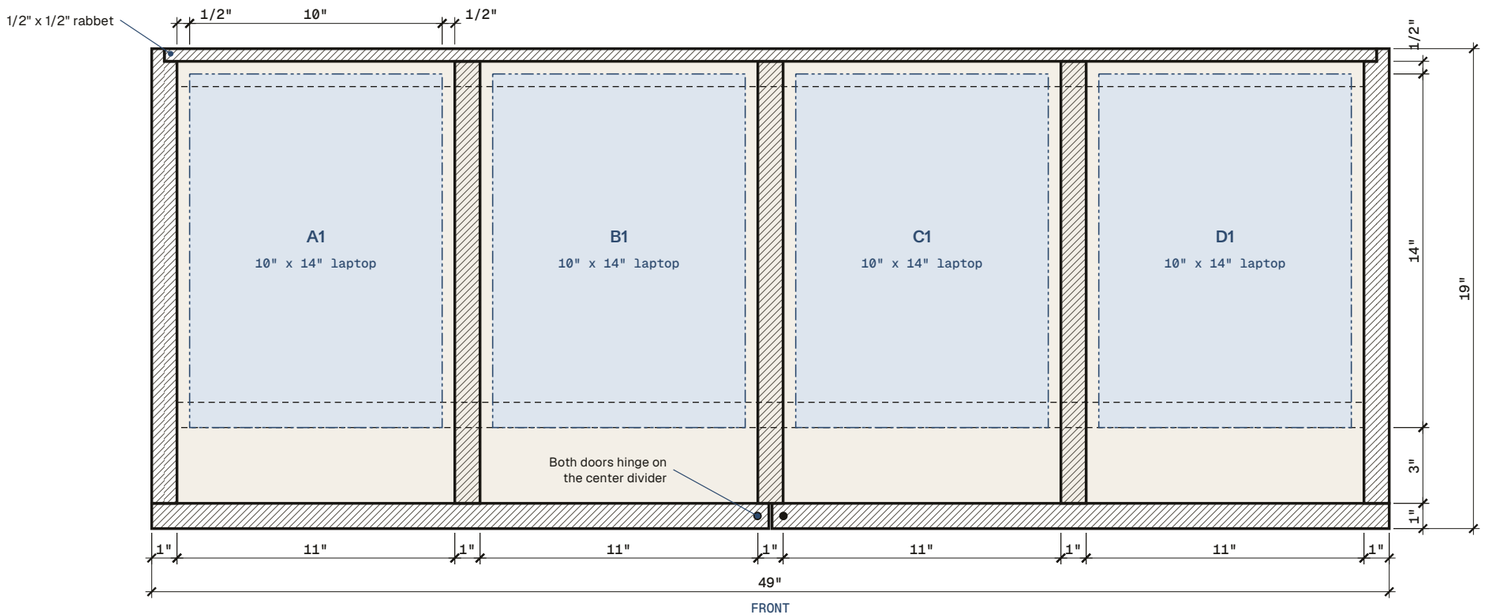

7 Plan section B-B

SCALE 1:6 · THROUGH TIER 1, LOOKING DOWN

OF4S

Office Furniture 4 Sale
1790 W 8th Ave, Hialeah, FL 33010
+1 305 889 3364 · officefurniture4sale.com

PROJECT
LC-60 laptop storage cabinet

CLIENT
To be confirmed

DRAWING
Top plan, plan section B-B

SCALE
1:6 at 11 x 17

DATE
Nov 9, 2026

REVISION
2 · Two doors, center hinged

UNITS
Inches. Use written dimensions; do not scale.

STATUS
For quotation. Fabricator submits shop drawings and finish samples for approval before production.

REV · DATE · DESCRIPTION

0 · 11/04/26 · Issued for pricing
1 · 11/04/26 · Doors in base scope; depth 16" to 18"; stacks to rear
2 · 11/09/26 · Two doors, both hinged on center divider, swing outward

SHEET
A-104

CAPACITY

Interior elevation, loaded



8 **Interior elevation, loaded**

SCALE 1:5 · DOORS REMOVED

BAY SCHEDULE

BAY	TIER FLOOR	LAPTOPS
A3	+25"	5
B3	+25"	5
C3	+25"	5
D3	+25"	5
A2	+15"	5
B2	+15"	5
C2	+15"	5
D2	+15"	5
A1	+5"	5
B1	+5"	5
C1	+5"	5
D1	+5"	5
Total		**60**

Bay IDs run A to D left to right, 1 to 3 bottom to top; the left door covers columns A and B, the right door C and D. Optional ID plates are ALT-4.

OF4S

Office Furniture 4 Sale
1790 W 8th Ave, Hialeah, FL 33010
+1 305 889 3364 · officefurniture4sale.com

PROJECT
LC-60 laptop storage cabinet

CLIENT
To be confirmed

DRAWING
Interior elevation, loaded

SCALE
1:5 at 11 x 17

DATE
Nov 9, 2026

REVISION
2 · Two doors, center hinged

UNITS
Inches. Use written dimensions; do not scale.

STATUS
For quotation. Fabricator submits shop drawings and finish samples for approval before production.


REV · DATE · DESCRIPTION

0 · 11/04/26 · Issued for pricing
1 · 11/04/26 · Doors in base scope; depth 16" to 18"; stacks to rear
2 · 11/09/26 · Two doors, both hinged on center divider, swing outward


SHEET
A-105

3D VIEWS


Isometric views

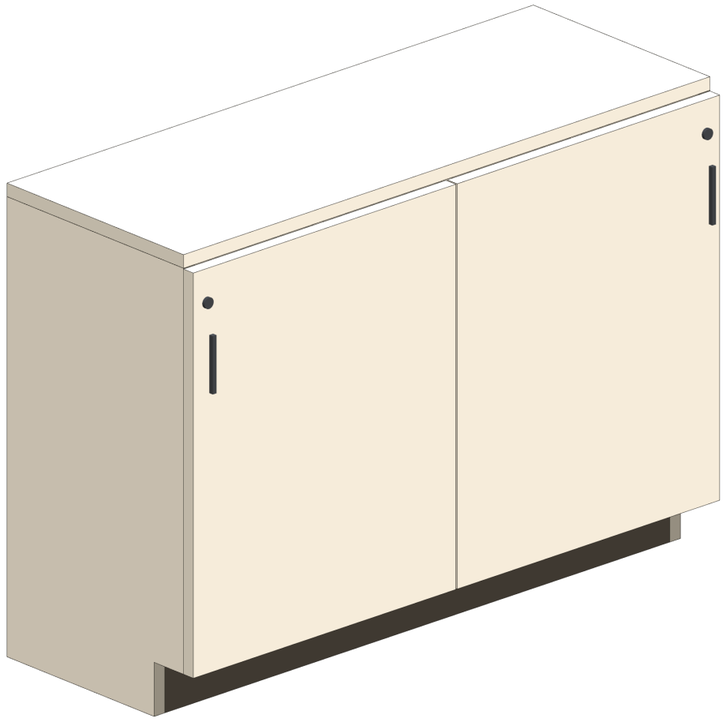


FRONT ISOMETRIC · DOORS CLOSED

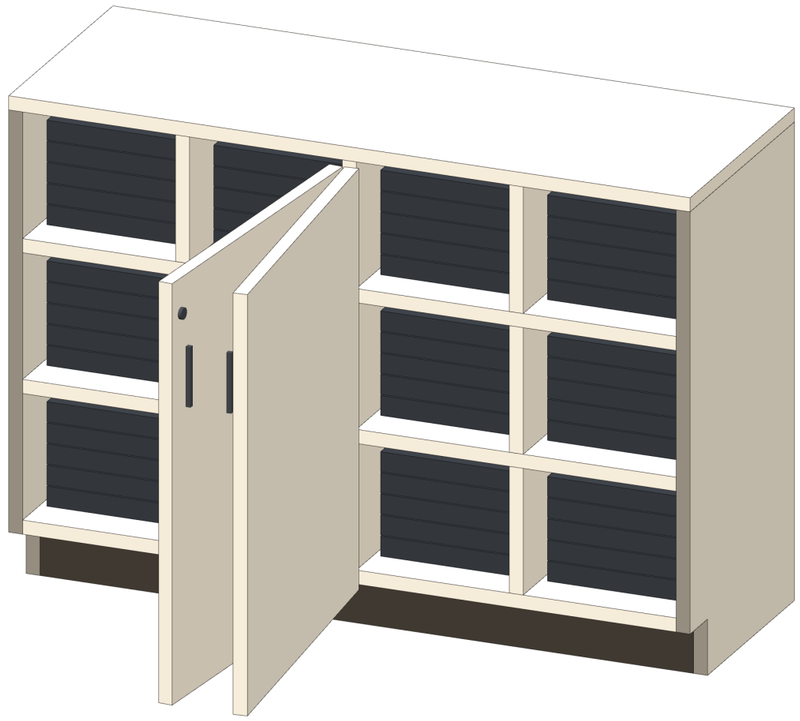

DOORS OPEN · LOADED WITH 60 LAPTOPS

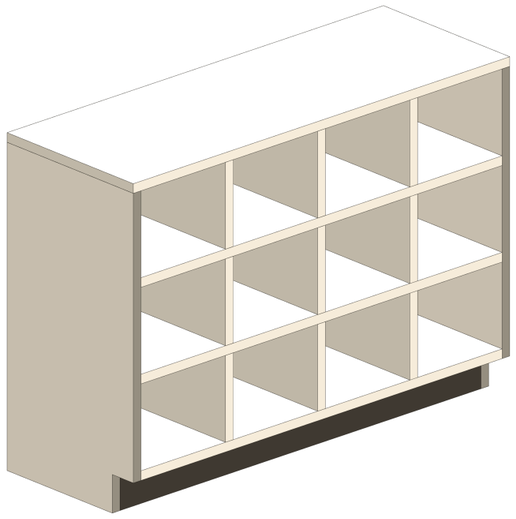

DOORS REMOVED · BAYS AND DIVIDERS

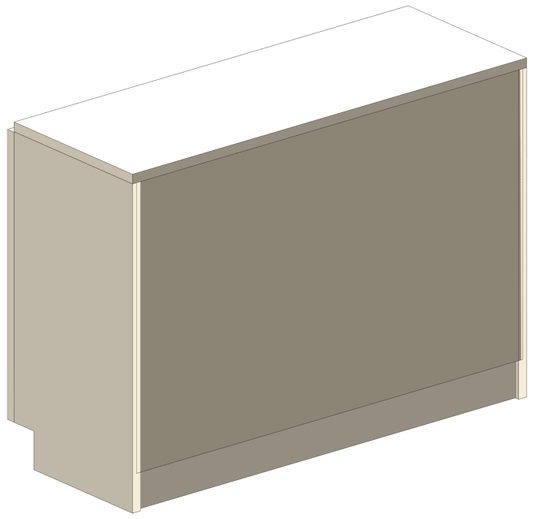

REAR ISOMETRIC · BACK PANEL AND REAR RAIL

OF4S

Office Furniture 4 Sale
1790 W 8th Ave, Hialeah, FL 33010
+1 305 889 3364 · officefurniture4sale.com

PROJECT
LC-60 laptop storage cabinet

CLIENT
To be confirmed

DRAWING
Isometric views

SCALE
Not to scale

DATE
Nov 9, 2026

REVISION
2 · Two doors, center hinged

UNITS
Inches. Use written dimensions; do not scale.

STATUS
For quotation. Fabricator submits shop drawings and finish samples for approval before production.


REV · DATE · DESCRIPTION

0 · 11/04/26 · Issued for pricing
1 · 11/04/26 · Doors in base scope; depth 16" to 18"; stacks to rear
2 · 11/09/26 · Two doors, both hinged on center divider, swing outward

SHEET
A-201

ASSEMBLY

Exploded isometric

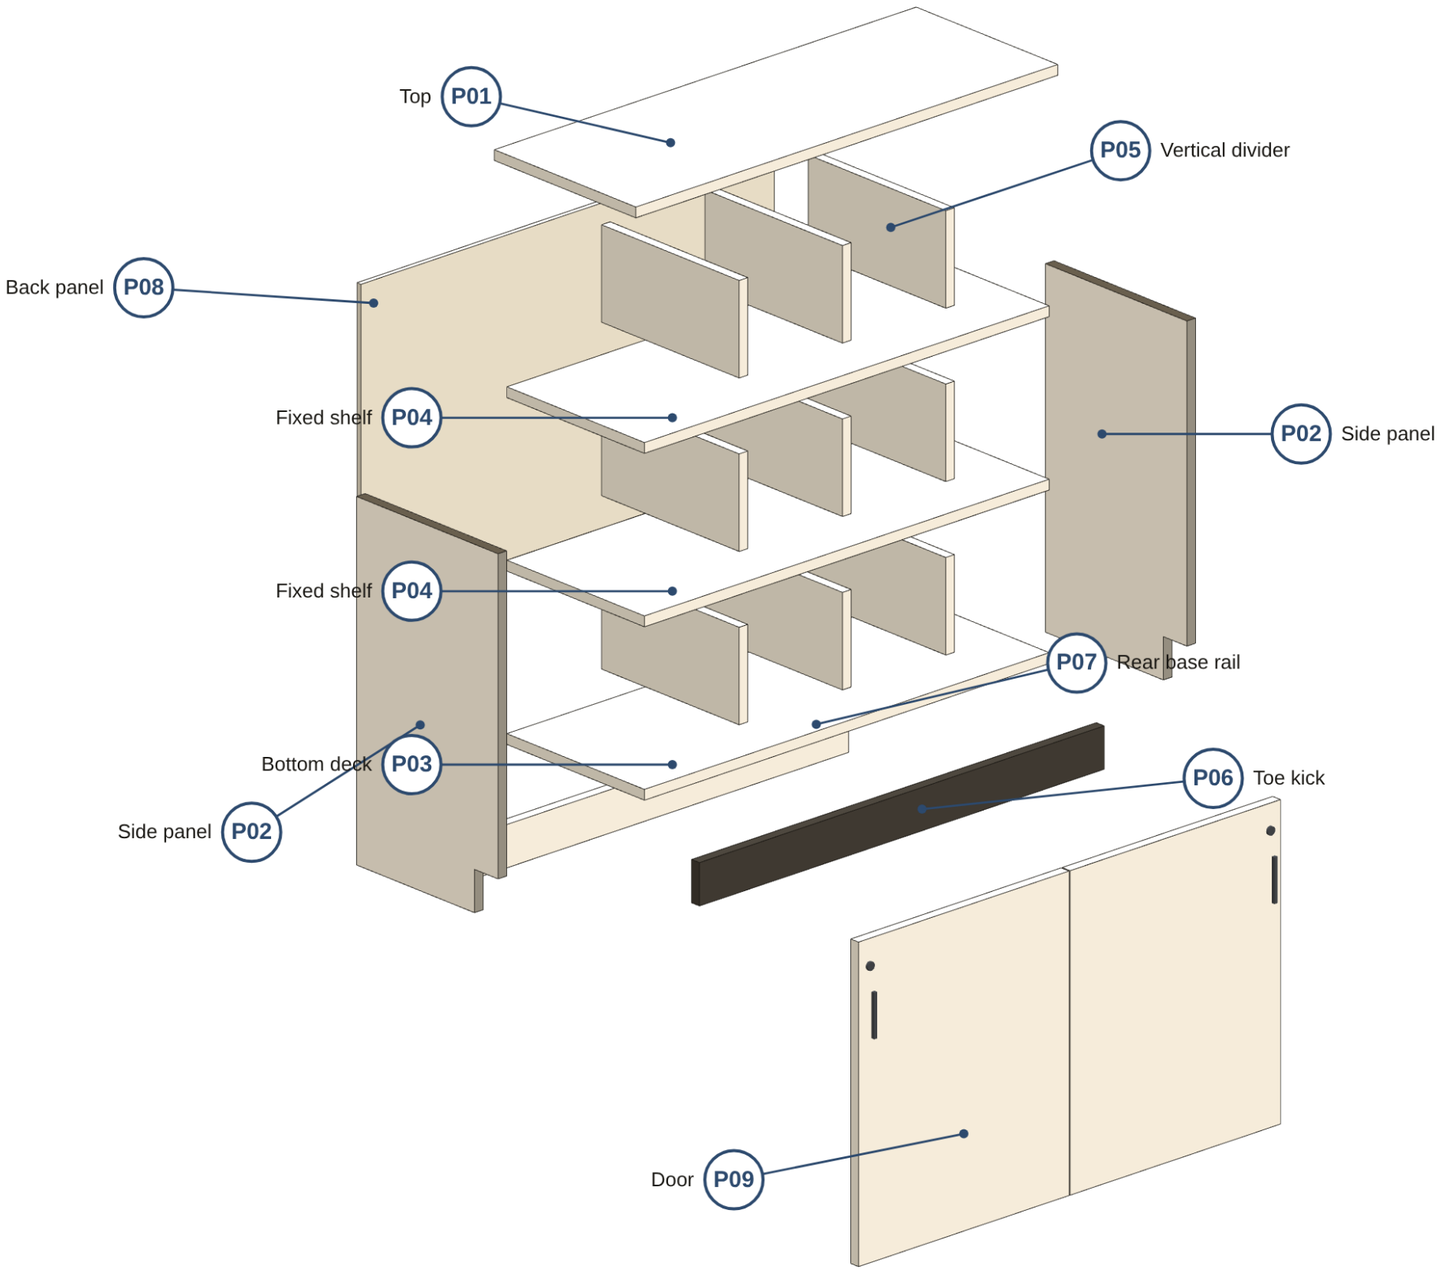

PART LEGEND

P01	**Top**	Qty 1 · 49" x 18" x 1"
P02	**Side panel**	Qty 2 · 34" x 18" x 1"
P03	**Bottom deck**	Qty 1 · 47" x 17-1/2" x 1"
P04	**Fixed shelf**	Qty 2 · 47" x 17-1/2" x 1"
P05	**Vertical divider**	Qty 9 · 9" x 17-1/2" x 1"
P06	**Toe kick**	Qty 1 · 47" x 4" x 1"
P07	**Rear base rail**	Qty 1 · 47" x 4" x 1"
P08	**Back panel**	Qty 1 · 48" x 30" x 1/2"
P09	**Door**	Qty 2 · 29-15/16" x 24-7/16" x 1"

ASSEMBLY SEQUENCE

1. Band edges; drill per A-301 to A-303.
2. Sides to bottom deck, toe kick, rear rail.
3. Tier 1 dividers, then shelf 1.
4. Tier 2 dividers, then shelf 2.
5. Tier 3 dividers, then top.
6. Square up; fit back into rabbets.
7. Hang doors; set locks, pulls, bumpers.
8. Glides; anti-tip kit on site.

OF4S

Office Furniture 4 Sale
1790 W 8th Ave, Hialeah, FL 33010
+1 305 889 3364 · officefurniture4sale.com

PROJECT
LC-60 laptop storage cabinet

CLIENT
To be confirmed

DRAWING
Exploded isometric

SCALE
Not to scale

DATE
Nov 9, 2026

REVISION
2 · Two doors, center hinged

UNITS
Inches. Use written dimensions; do not scale.

STATUS
For quotation. Fabricator submits shop drawings and finish samples for approval before production.

REV · DATE · DESCRIPTION

0 · 11/04/26 · Issued for pricing
1 · 11/04/26 · Doors in base scope; depth 16" to 18"; stacks to rear
2 · 11/09/26 · Two doors, both hinged on center divider, swing outward

SHEET
A-202


PART DETAILS

Top, side, bottom deck, shelf

Edgeband, 3 mm PVC · Mating part location · Hidden


P01 Top

QTY 1 · 1" THICK · 1" TFM BOARD · SCALE 1:8

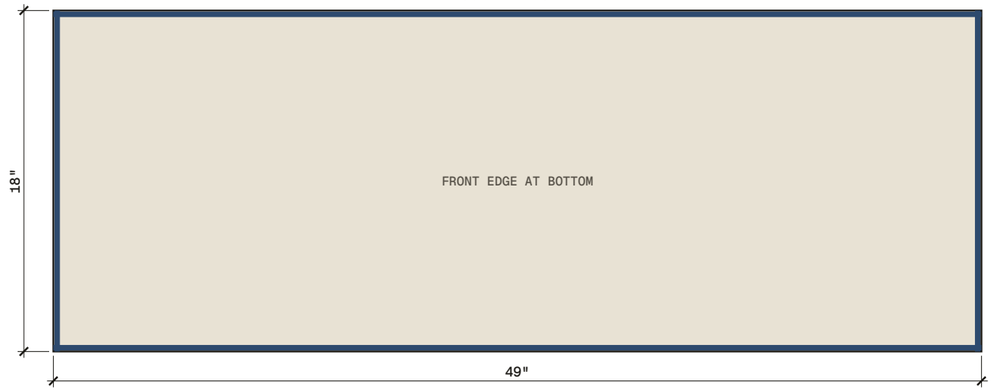


P03 Bottom deck


QTY 1 · 1" THICK · 1" TFM BOARD · SCALE 1:8

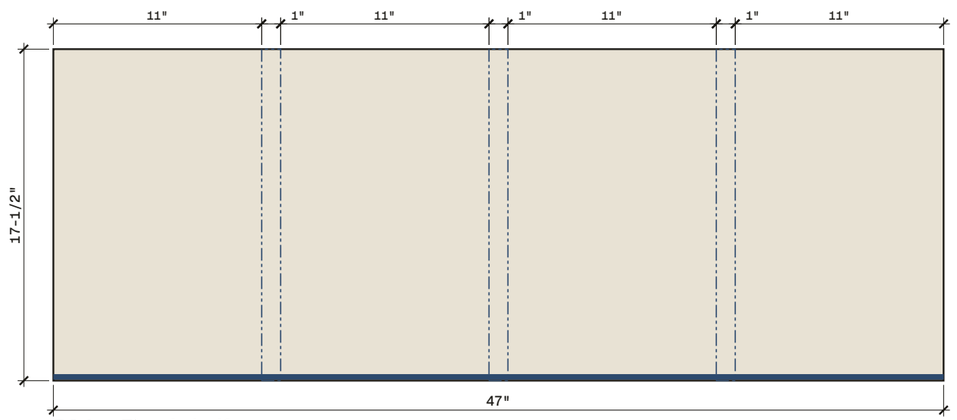

P04 Fixed shelf

QTY 2 · 1" THICK · 1" TFM BOARD · SCALE 1:8

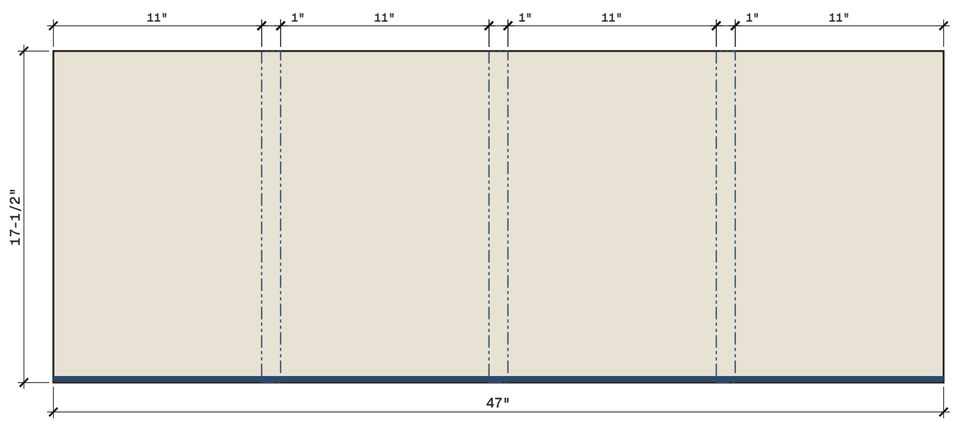

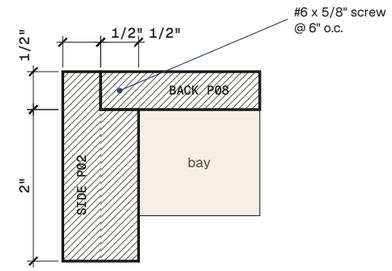


9 Rabbet

PLAN DETAIL, SCALE 1:2

P02 Side panel (left & right, mirror pair)

QTY 2 · 1" THICK · 1" TFM BOARD · SCALE 1:8

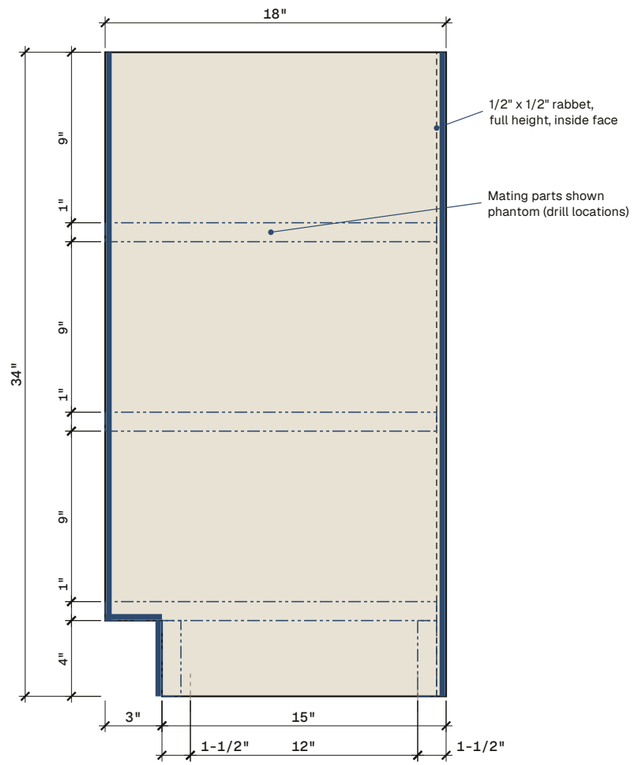

Shown: right side, viewed from outside. Left side is the mirror.

OF4S

Office Furniture 4 Sale
1790 W 8th Ave, Hialeah, FL 33010
+1 305 889 3364 · officefurniture4sale.com

PROJECT
LC-60 laptop storage cabinet

CLIENT
To be confirmed

DRAWING
Part details 1

SCALE
1:8, 1:2 at 11 x 17

DATE
Nov 9, 2026

REVISION
2 · Two doors, center hinged

UNITS
Inches. Use written dimensions; do not scale.

STATUS
For quotation. Fabricator submits shop drawings and finish samples for approval before production.

REV · DATE · DESCRIPTION

0 · 11/04/26 · Issued for pricing
1 · 11/04/26 · Doors in base scope; depth 16" to 18"; stacks to rear
2 · 11/09/26 · Two doors, both hinged on center divider, swing outward

SHEET
A-301


PART DETAILS

Divider, toe kick, rear rail, back panel

Edgeband, 3 mm PVC · Mating part location · Hidden


P08 Back panel

QTY 1 · 1/2" THICK · 1/2" TFM BACK · SCALE 1:8

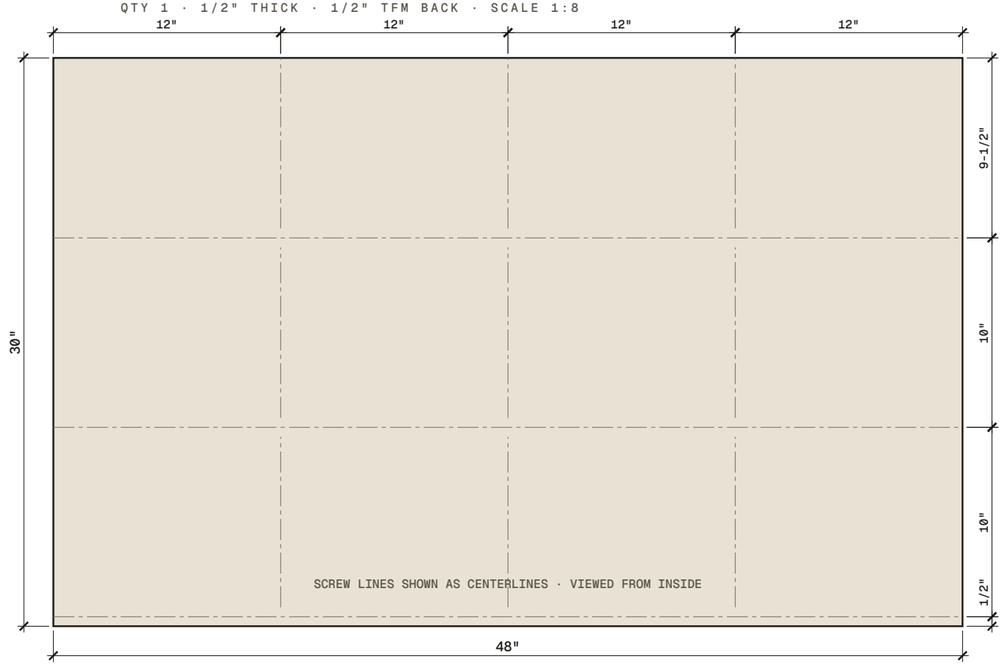


P06 Toe kick

QTY 1 · 1" THICK · 1" TFM BOARD · SCALE 1:8

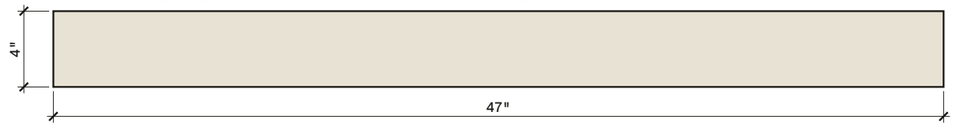


P07 Rear base rail

QTY 1 · 1" THICK · 1" TFM BOARD · SCALE 1:8

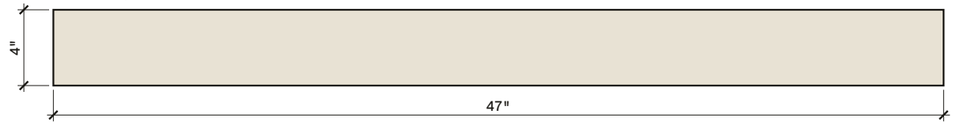

P05 Vertical divider

QTY 9 · 1" THICK · 1" TFM BOARD · SCALE 1:8

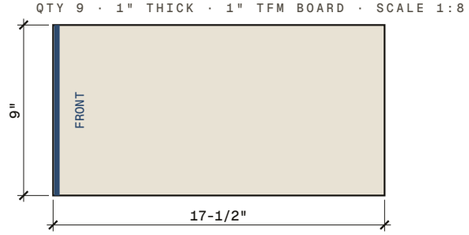

JOINERY AND MACHINING

- Dividers: two 8 mm dowels each end into shelf or deck, glued. Align in one vertical line per column.
- Top, deck, shelves, toe kick and rear rail to sides: dowels plus 7 x 50 mm confirmat screws, 3 per joint (2 at kick and rail). Cap exposed heads.
- Back panel: screwed into rabbets and along the centerlines shown, #6 x 5/8" at 6" o.c.
- Toe kick and rear rail are not edgebanded. Toe kick face in black or dark laminate if available.
- Glides: threaded inserts in side bottom edges at the locations on A-301.
- Tolerances: parts +/- 1/32". Assembled carcass square within 1/16" on diagonals.

OF4S

Office Furniture 4 Sale
1790 W 8th Ave, Hialeah, FL 33010
+1 305 889 3364 · officefurniture4sale.com

PROJECT
LC-60 laptop storage cabinet

CLIENT
To be confirmed

DRAWING
Part details 2

SCALE
1:8 at 11 x 17

DATE
Nov 9, 2026

REVISION
2 · Two doors, center hinged

UNITS
Inches. Use written dimensions; do not scale.

STATUS
For quotation. Fabricator submits shop drawings and finish samples for approval before production.

REV · DATE · DESCRIPTION

0 · 11/04/26 · Issued for pricing
1 · 11/04/26 · Doors in base scope; depth 16" to 18"; stacks to rear
2 · 11/09/26 · Two doors, both hinged on center divider, swing outward

SHEET
A-302


PART DETAILS

Doors

Edgeband, 3 mm PVC Mating part location Hidden

P09 Door (left & right, mirror pair)

QTY 2 · 1" THICK · 1" TFM BOARD · SCALE 1:4

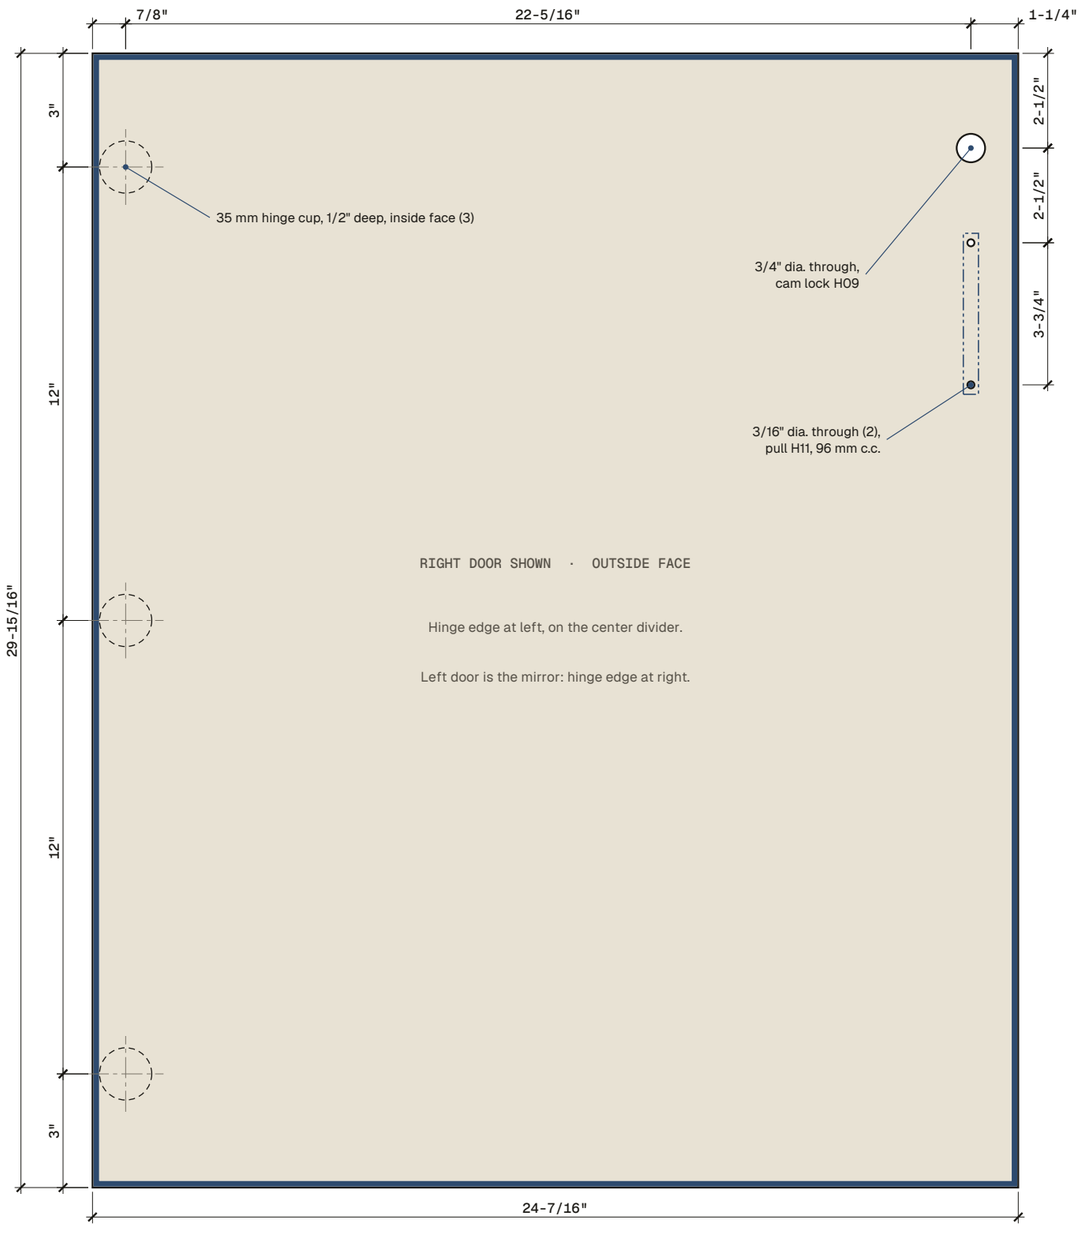

DOOR SCHEDULE

DOOR	PART	WIDTH	COVERS	HINGED ON	LOCK AT
Left	P09	24-7/16"	A and B	Center divider, left face	Left side
Right	P09	24-7/16"	C and D	Center divider, right face	Right side

DOOR NOTES

- 2 doors, each covering two columns, 1" TFM to match carcass, 3 mm PVC on all edges.
- Height 29-15/16": bottom flush with underside of deck (4" AFF), 1/16" below the top.
- Both doors hinge on the center divider and swing outward. 1/8" joint centered on the divider; free edges flush with the sides.
- 3 hinges per door (doors are 24-7/16" wide, about 20 lb each). Middle hinge at mid-height lands on the tier-2 divider; top and bottom hinges on tiers 3 and 1.
- One door alone opens to 110°. With both open they stand back to back at about 85°, so pulls are on the outer edge only. Allow 26" clear in front (A-501).
- Locks keyed alike: 2 keys per lock plus a master. Strike on the side panel behind each free edge.
- 2 clear bumpers per door on the back face at the free edge.
- Make one left and one right door: same size, mirrored drilling.

OF4S

Office Furniture 4 Sale
1790 W 8th Ave, Hialeah, FL 33010
+1 305 889 3364 · officefurniture4sale.com

PROJECT
LC-60 laptop storage cabinet

CLIENT
To be confirmed

DRAWING
Door details

SCALE
1:4 at 11 x 17

DATE
Nov 9, 2026

REVISION
2 · Two doors, center hinged

UNITS
Inches. Use written dimensions; do not scale.

STATUS
For quotation. Fabricator submits shop drawings and finish samples for approval before production.

REV · DATE · DESCRIPTION

0 · 11/04/26 · Issued for pricing
1 · 11/04/26 · Doors in base scope; depth 16" to 18"; stacks to rear
2 · 11/09/26 · Two doors, both hinged on center divider, swing outward

SHEET
A-303

BILL OF MATERIALS

Cut list, hardware and materials

CUT LIST · FINISHED SIZES, INCLUDING EDGEBAND

MARK	PART	QTY	LENGTH	WIDTH	THK	MATL	EDGEBAND	NOTES	SQ FT
P01	Top	1	49"	18"	1"	M1	All 4 edges	Sits on top of side panels. Flush front, back and ends. Band all 4 edges.	6.1
P02	Side panel (left & right, mirror pair)	2	34"	18"	1"	M1	Front, rear, notch	Toe-kick notch 3" deep x 4" high at front bottom. 1/2" x 1/2" rabbet full height on rear inside edge for back panel. Make one left and one right.	8.5
P03	Bottom deck	1	47"	17-1/2"	1"	M1	Front	Between sides, top surface at 5" AFF. Band front edge.	5.7
P04	Fixed shelf	2	47"	17-1/2"	1"	M1	Front	Fixed (not adjustable). Supported by dividers below every 12". Band front edge.	11.4
P05	Vertical divider	9	9"	17-1/2"	1"	M1	Front	Grain/length vertical. 3 per tier, stacked in line. Band front edge.	9.8
P06	Toe kick	1	47"	4"	1"	M1	None	Between sides, front face recessed 3" (flush with notch).	1.3
P07	Rear base rail	1	47"	4"	1"	M1	None	Between sides under rear of bottom deck, back face flush with back of deck.	1.3
P08	Back panel	1	48"	30"	1/2"	M2	None	Captured in side rabbets, screwed to rear edges of deck, shelves and dividers #6 x 5/8" pan head at 6" o.c.	10.0
P09	Door (left & right, mirror pair)	2	29-15/16"	24-7/16"	1"	M1	All 4 edges	Both hinged on the center divider (half overlay), swinging outward; free edge flush with the side. 3 x 35 mm hinge cups (inside face), 3/4" lock hole and 2 pull holes at the free edge. Make one left and one right. See A-303. Band all 4 edges.	10.2

HARDWARE

MARK	ITEM	QTY	NOTES
H01	Leveling glide, 5/16"-18, 1-1/4" dia. nylon base, with threaded insert	4	Into bottom edge of each side panel, 2 per side. Adds about 3/8" (see note 6).
H02	8 mm x 35 mm fluted hardwood dowel	60	Divider ends (2 per end) and carcass joints. Glued.
H03	7 x 50 mm confirmat screw (or cam + bolt if shipped knock-down)	36	Sides to top, bottom deck, shelves, toe kick and rear rail. Heads capped.
H04	Confirmat cover cap, color-matched	36	Exposed screw heads on side panels.
H05	#6 x 5/8" pan-head screw	40	Back panel to rabbets and rear edges, 6" o.c.
H06	Anti-tip wall bracket kit (pair) with fasteners	1	Under top at rear. Required: loaded weight over 500 lb and doors swing forward.
H07	3 mm PVC, color-matched, radiused 1/16" (≈ 1 mm)	66 LF	See cut list for linear feet.
H08	Concealed hinge, 35 mm cup, 110° soft-close, half overlay, clip-on, with mounting plate	6	3 per door, all on the center divider (left door on its left face, right door on its right face). Fabricator to select crank for a 7/16" overlay on the 1" divider.
H09	Cam lock, 3/4" body, keyed alike, 2 keys per lock + master	2	1 per door at the outer (free) edge, 2-1/2" from top.
H10	L-strike for cam lock	2	On the inside face of each side panel, behind the door's free edge.
H11	Wire pull, 96 mm (3-3/4") c.c., brushed nickel or black	2	1 per door, vertical, at the outer (free) edge.
H12	Clear door bumper, 3/8" dia.	4	2 per door, back face, free edge.

MATERIAL SUMMARY

CODE	MATERIAL	NET AREA	EST. SHEETS
M1	1" industrial particleboard core, thermally fused laminate (TFM) both faces	54.4 sf	3 @ 49" x 97"
M2	1/2" MDF, TFM both faces (interior face to match carcass)	10.0 sf	1 @ 49" x 97"
EB	3 mm PVC, color-matched, radiused 1/16" (≈ 1 mm)	59.6 LF	66 LF w/ 10%
	Weight, empty / loaded (approx.)	233 lb	533 lb

Sheet counts are a nesting estimate for quoting. Fabricator to optimize. Color: by owner, to be confirmed. Quote standard TFM colors at no upcharge.

OF4S

Office Furniture 4 Sale
1790 W 8th Ave, Hialeah, FL 33010
+1 305 889 3364 · officefurniture4sale.com

PROJECT
LC-60 laptop storage cabinet

CLIENT
To be confirmed

DRAWING
Cut list and hardware

SCALE
None

DATE
Nov 9, 2026

REVISION
2 · Two doors, center hinged

UNITS
Inches. Use written dimensions; do not scale.

STATUS
For quotation. Fabricator submits shop drawings and finish samples for approval before production.


REV · DATE · DESCRIPTION

0 · 11/04/26 · Issued for pricing
1 · 11/04/26 · Doors in base scope; depth 16" to 18"; stacks to rear
2 · 11/09/26 · Two doors, both hinged on center divider, swing outward

SHEET
A-401

QUOTATION

Alternates and quote request

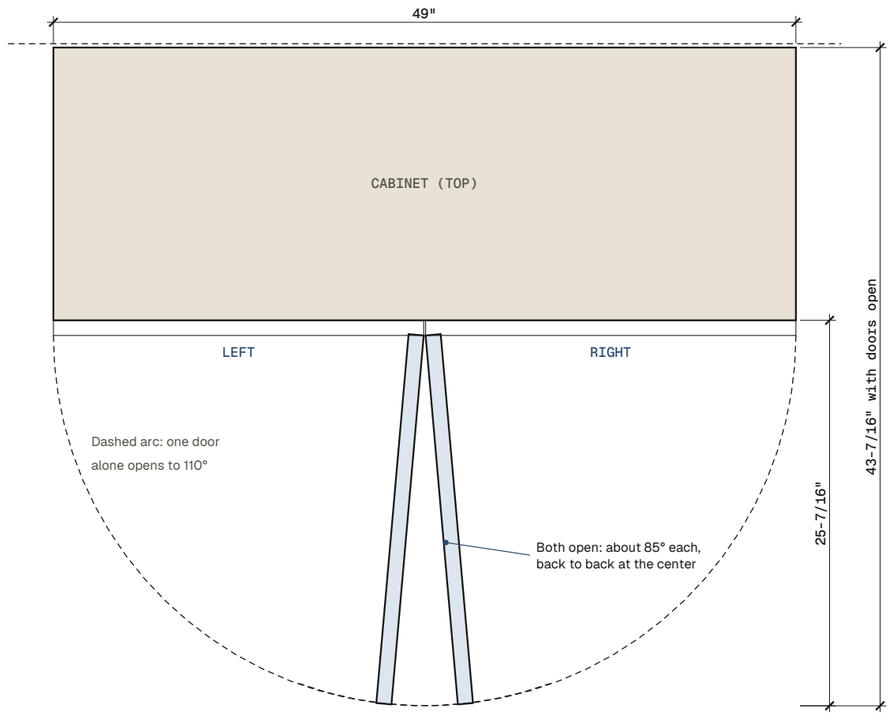

10 **Door swing plan**

BOTH DOORS AT 85°, SCALE 1:10

ALTERNATES · PRICE EACH SEPARATELY, PER CABINET

ALT-1 **Ventilation**
One 2" dia. grommet with cap through the back panel at each bay (12), or routed vent slots per bay. Not needed while laptops are stored cold; useful if they go in warm.

ALT-2 **Charging**
Not in scope: the client has not asked for charging. If needed later, quote a UL-listed charging solution separately (power strips inside casework are not code-compliant).

ALT-3 **Mobile base**
Replace toe kick and rear rail with a 1" sub-base on 4 x 3" locking casters, keeping 35" overall height.

ALT-4 **Bay labels**
Engraved or printed ID plates A1 to D3 on shelf fronts (12), plus Left and Right on the door fronts (2).

ALT-5 **Master-keyed locks**
Locks keyed differently per door with one master key, instead of keyed alike.

PLEASE QUOTE

1. Unit price for the base cabinet as drawn, including the 2 lockable doors and door hardware, at quantities of 1, 2 and 5.
2. Each alternate (ALT-1 to ALT-5) as a separate add per cabinet.
3. Freight to 1790 W 8th Ave, Hialeah, FL 33010, and whether it ships assembled or knock-down.
4. Lead time from shop-drawing approval.
5. Standard laminate colors available at no upcharge, and edgeband match.
6. Warranty terms.
7. Any change you recommend for cost or strength (for example 3/4" dividers). Price it as a voluntary alternate; do not substitute in the base price.

OPEN ITEMS · OWNER TO CONFIRM BEFORE RELEASE

- Exact laptop model and size, with or without a protective case.
- Charging inside the cabinet is assumed not required. Confirm.
- Door pull and lock finish (brushed nickel or black).
- Is 35" a hard maximum (under a window or counter)? Glides add about 3/8".
- Wall-mounted location, or freestanding with a finished back?
- Laminate color and number of cabinets.

CONTACT

Office Furniture 4 Sale · +1 305 889 3364
officefurniture4sale.com

OF4S

Office Furniture 4 Sale
1790 W 8th Ave, Hialeah, FL 33010
+1 305 889 3364 · officefurniture4sale.com

PROJECT
LC-60 laptop storage cabinet

CLIENT
To be confirmed

DRAWING
Alternates, quote request

SCALE
1:10 at 11 x 17

DATE
Nov 9, 2026

REVISION
2 · Two doors, center hinged

UNITS
Inches. Use written dimensions; do not scale.

STATUS
For quotation. Fabricator submits shop drawings and finish samples for approval before production.

REV · DATE · DESCRIPTION

0 · 11/04/26 · Issued for pricing
1 · 11/04/26 · Doors in base scope; depth 16" to 18"; stacks to rear
2 · 11/09/26 · Two doors, both hinged on center divider, swing outward

SHEET
A-501
13 of 13