CUSTOM CASEWORK · REQUEST FOR QUOTATION

LC-60 laptop storage cabinet


Sixty laptops in twelve open bays of five. 49" wide, 16" deep, 35" tall. Fixed shelves, 1" panels throughout, 4" toe-kick base.

DESIGN BASIS

Laptop footprint	10" x 14", 1-1/2" thick
Stack limit	5 laptops = 7-1/2" tall
Capacity	60 laptops = 12 stacks (required 60)
Layout	4 columns x 3 tiers = 12 bays
Clear bay	11" W x 9" H x 15-1/2" D
Clearance per stack	1/2" each side, 1-1/2" above, 3/4" front and back
Overall size	49" W x 16" D x 35" H
Panels	1" sides, top, deck, shelves, dividers. 1/2" back
Base	4" toe kick, recessed 3"; first bay floor at 5"
Weight (approx.)	175 lb empty, 475 lb loaded at 5 lb per laptop

GENERAL NOTES

1. All dimensions are finished sizes in inches. Overall height is floor to top of top, glides at minimum.
2. Board: 1" industrial particleboard, 45 lb density minimum, thermally fused laminate both faces. Back: 1/2" MDF, TFM both faces. Color by owner, to be confirmed.
3. Edgeband: 3 mm PVC on every exposed edge, color-matched. See cut list A-401.
4. Joinery: 8 mm dowels plus confirmat screws, factory assembled. Knock-down cam fittings acceptable if stated in the quote.
5. Shelves are fixed and carried by dividers every 12". Minimum 50 lb per bay.
6. Glides add about 3/8". If 35" is a hard maximum, cut toe kick, rear rail and notch to 3-5/8".
7. Anchor to the wall with the anti-tip kit (H06). Loaded weight is about 475 lb.
8. Confirm laptop size against an owner sample before cutting.

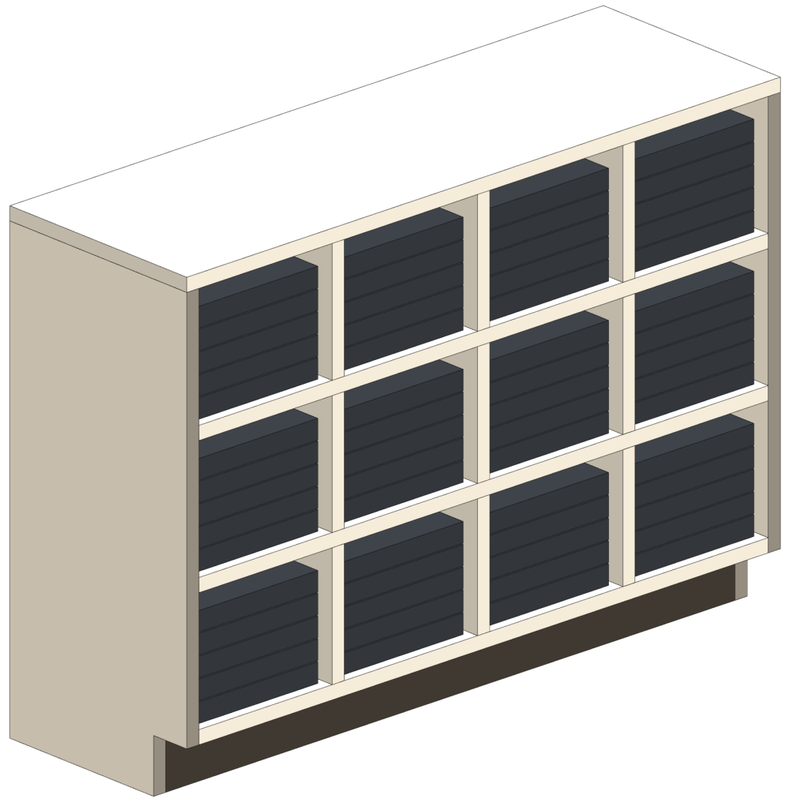

ISOMETRIC · SHOWN LOADED WITH 60 LAPTOPS

SHEET INDEX

A-001	Cover, design basis, notes	A-202	Exploded isometric
A-101	Front elevation	A-301	Part details 1
A-102	Section A-A, side elevation, bay	A-302	Part details 2
A-103	Top plan, plan section B-B	A-401	Cut list and hardware
A-104	Front elevation, loaded	A-501	Alternates, quote request
A-201	Isometric views		

OF4S

Office Furniture 4 Sale
1790 W 8th Ave, Hialeah, FL 33010
+1 305 889 3364 · officefurniture4sale.com

PROJECT
LC-60 laptop storage cabinet

CLIENT
To be confirmed

DRAWING
Cover, design basis, notes

SCALE
As noted

DATE
Nov 4, 2026

REVISION
0 · Issued for pricing

UNITS
Inches. Use written dimensions; do not scale.


STATUS
For quotation. Fabricator submits shop drawings and finish samples for approval before production.

REV · DATE · DESCRIPTION
0 · 11/04/26 · Issued for pricing

SHEET
A-001

ELEVATIONS

Front elevation

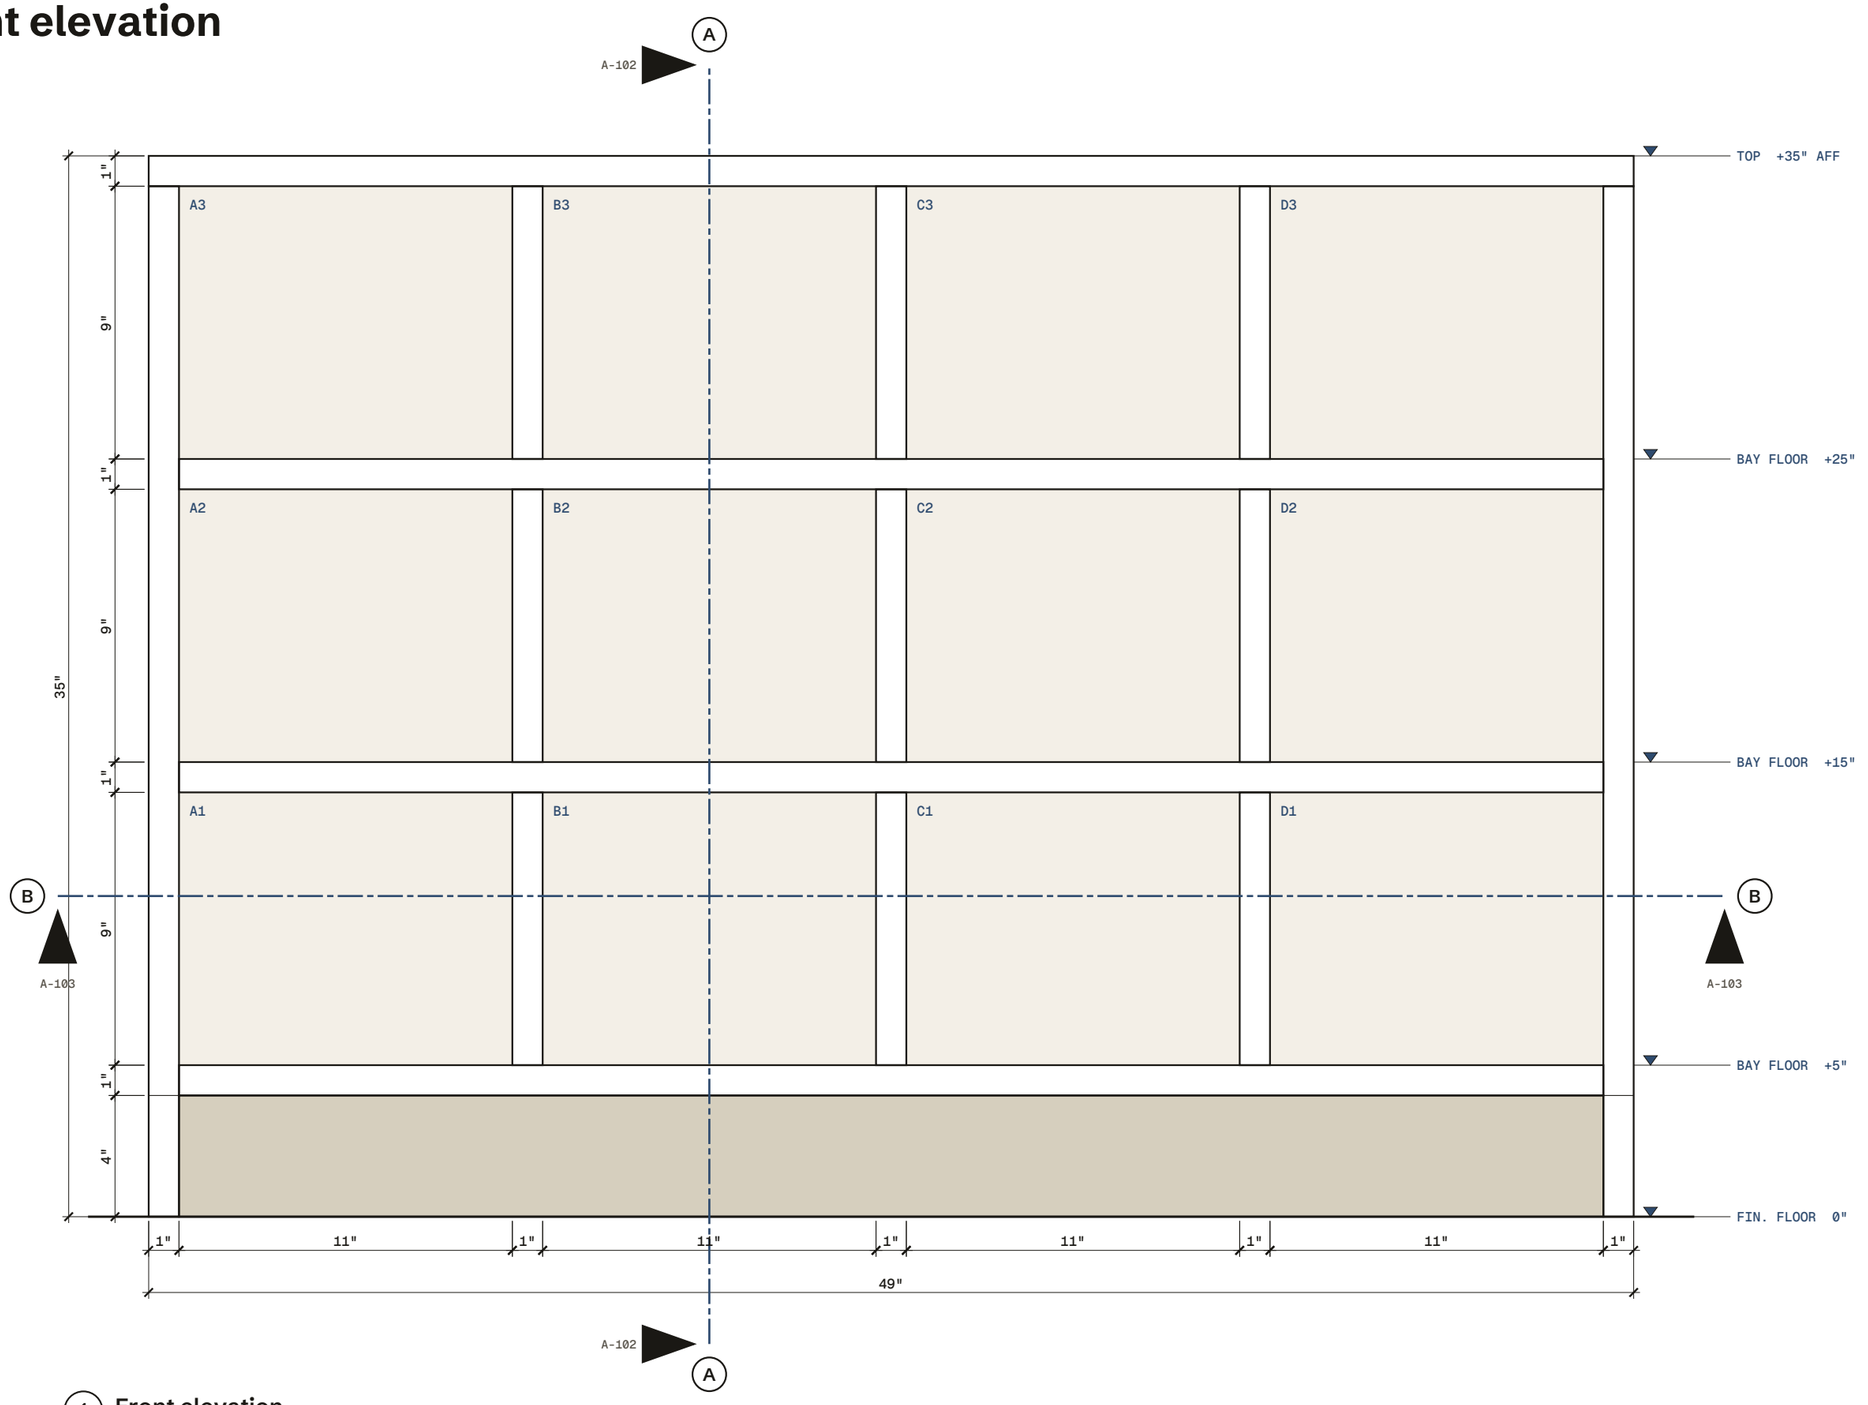

1 **Front elevation**

SCALE 1:5

OF4S

Office Furniture 4 Sale
1790 W 8th Ave, Hialeah, FL 33010
+1 305 889 3364 · officefurniture4sale.com

PROJECT
LC-60 laptop storage cabinet

CLIENT
To be confirmed

DRAWING
Front elevation

SCALE
1:5 at 11 x 17

DATE
Nov 4, 2026

REVISION
0 · Issued for pricing

UNITS
Inches. Use written dimensions; do not scale.


STATUS
For quotation. Fabricator submits shop drawings and finish samples for approval before production.

REV · DATE · DESCRIPTION
0 · 11/04/26 · Issued for pricing

SHEET
A-101


SECTIONS AND DETAILS

Section A-A, side elevation, bay detail

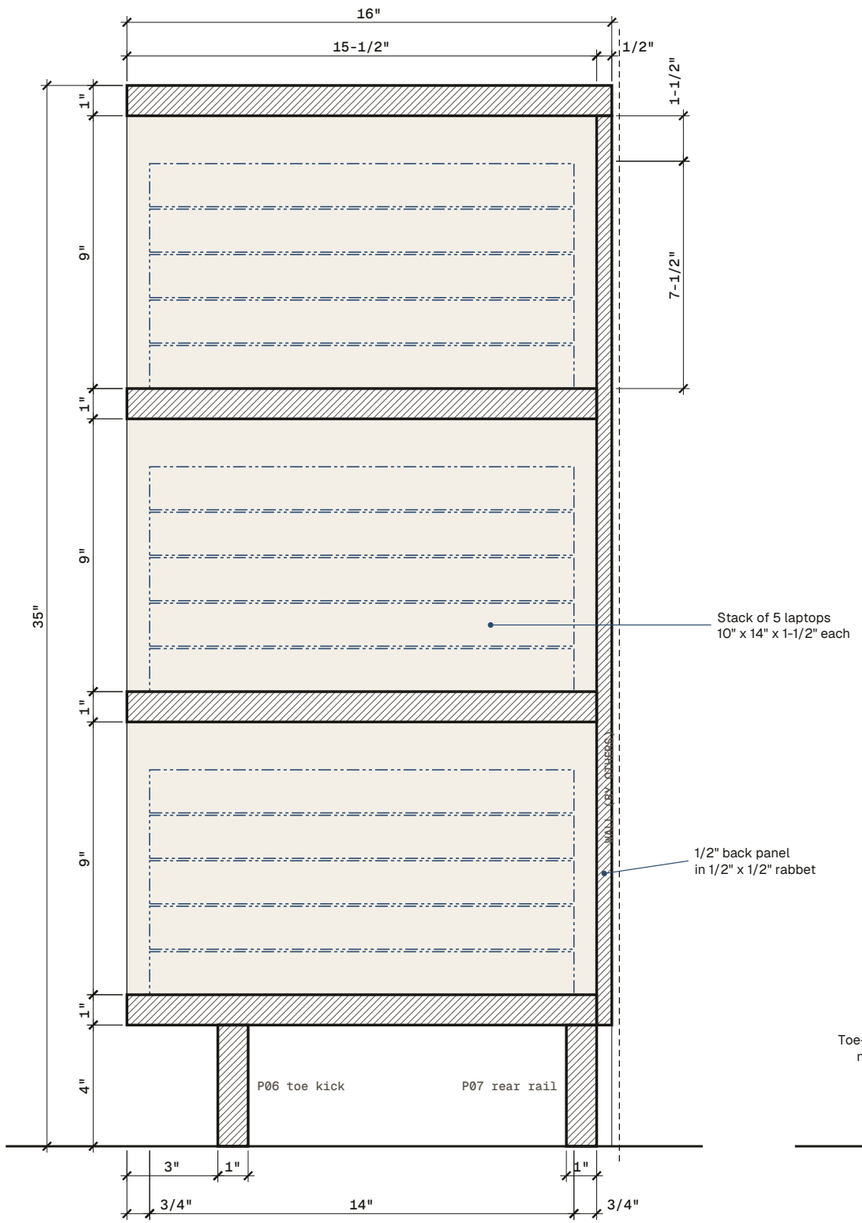


2 **Section A-A**

SCALE 1:5 · SEE A-101

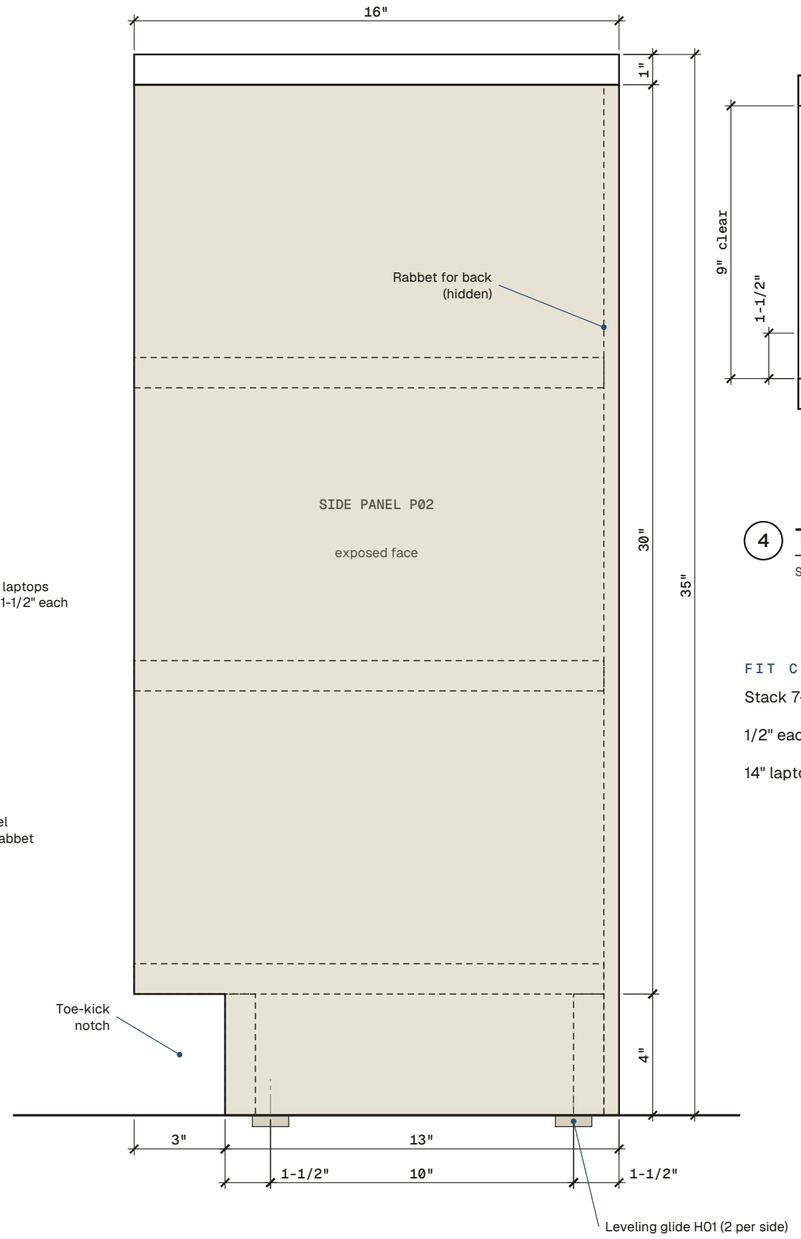

3 **Right side elevation**

SCALE 1:5 · LEFT SIDE MIRROR

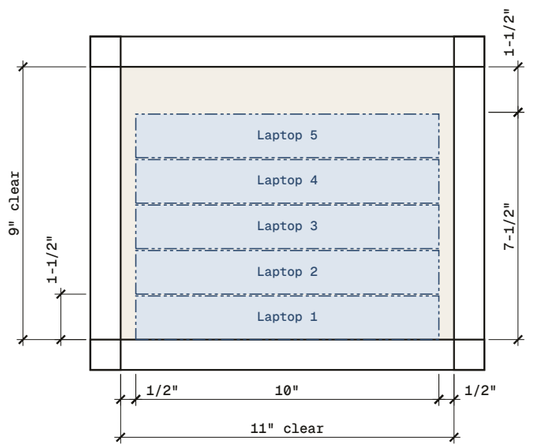

4 **Typical bay**

SCALE 1:5

FIT CHECK

Stack 7-1/2" in a 9" bay leaves 1-1/2" to lift the top laptop.

1/2" each side for fingers and rubber feet.

14" laptop in 15-1/2" depth: 1-1/2" spare.

OF4S

Office Furniture 4 Sale
1790 W 8th Ave, Hialeah, FL 33010
+1 305 889 3364 · officefurniture4sale.com

PROJECT
LC-60 laptop storage cabinet

CLIENT
To be confirmed

DRAWING
Section A-A, side elevation, bay

SCALE
1:5 at 11 x 17

DATE
Nov 4, 2026

REVISION
0 · Issued for pricing

UNITS
Inches. Use written dimensions; do not scale.


STATUS
For quotation. Fabricator submits shop drawings and finish samples for approval before production.

REV · DATE · DESCRIPTION
0 · 11/04/26 · Issued for pricing

SHEET
A-102


PLANS

Top plan and plan section B-B

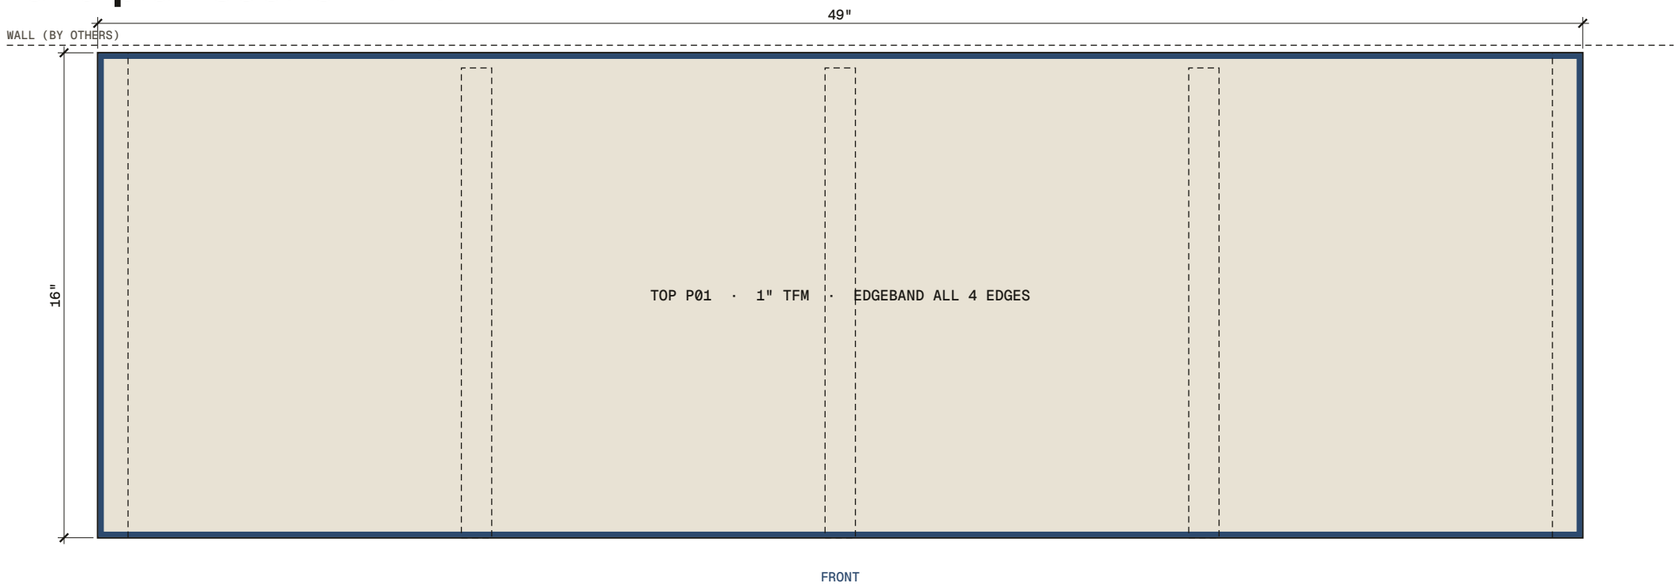

5 Top plan

SCALE 1:5

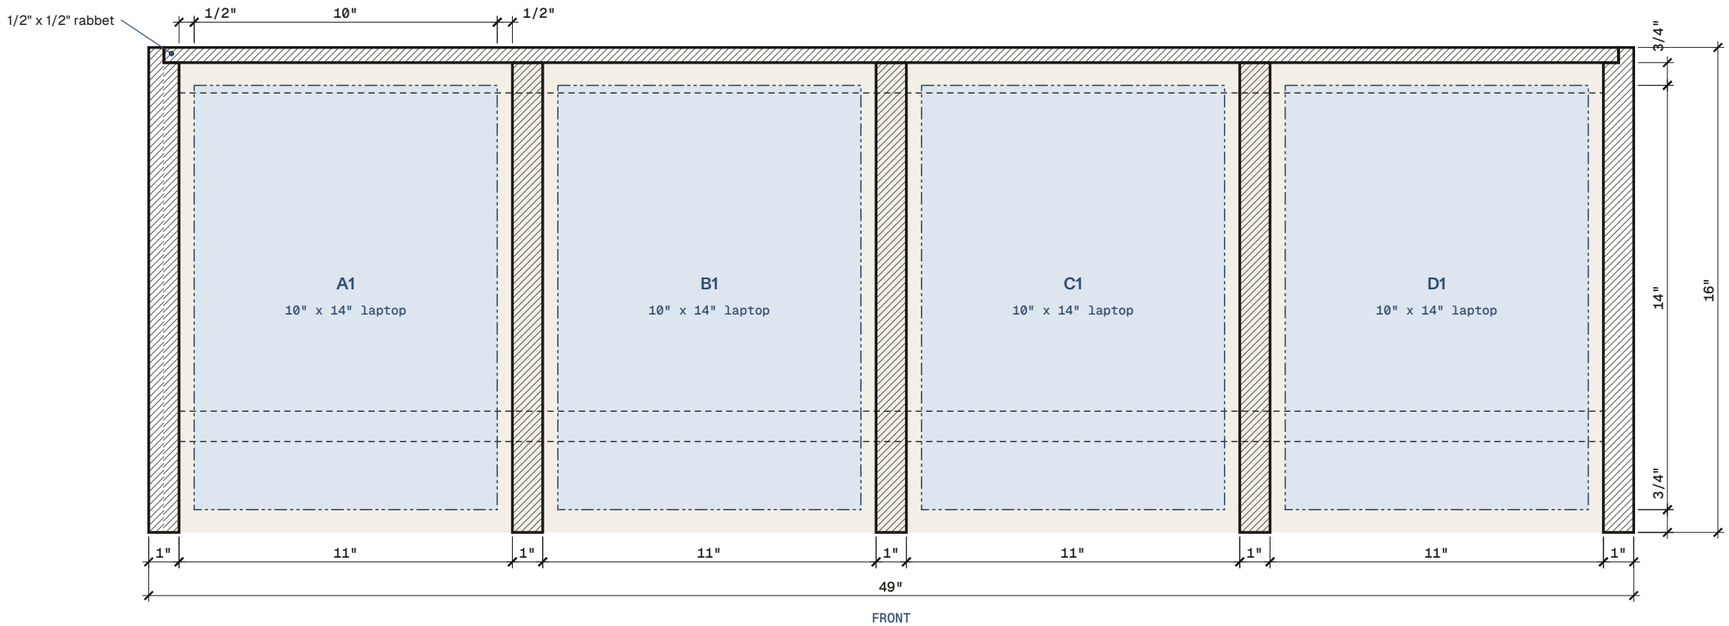

6 Plan section B-B

SCALE 1:5 · THROUGH TIER 1, LOOKING DOWN

OF4S

Office Furniture 4 Sale
1790 W 8th Ave, Hialeah, FL 33010
+1 305 889 3364 · officefurniture4sale.com

PROJECT
LC-60 laptop storage cabinet

CLIENT
To be confirmed

DRAWING
Top plan, plan section B-B

SCALE
1:5 at 11 x 17

DATE
Nov 4, 2026

REVISION
0 · Issued for pricing

UNITS
Inches. Use written dimensions; do not scale.

STATUS
For quotation. Fabricator submits shop drawings and finish samples for approval before production.

REV · DATE · DESCRIPTION
0 · 11/04/26 · Issued for pricing

SHEET
A-103

CAPACITY

Front elevation, loaded



BAY SCHEDULE

BAY	TIER FLOOR	LAPTOPS
A3	+25"	5
B3	+25"	5
C3	+25"	5
D3	+25"	5
A2	+15"	5
B2	+15"	5
C2	+15"	5
D2	+15"	5
A1	+5"	5
B1	+5"	5
C1	+5"	5
D1	+5"	5
Total		**60**

Bay IDs run A to D left to right, 1 to 3 bottom to top. Optional ID plates are ALT-5.

7 **Front elevation, loaded**

SCALE 1:5

OF4S

Office Furniture 4 Sale
1790 W 8th Ave, Hialeah, FL 33010
+1 305 889 3364 · officefurniture4sale.com

PROJECT
LC-60 laptop storage cabinet

CLIENT
To be confirmed

DRAWING
Front elevation, loaded

SCALE
1:5 at 11 x 17

DATE
Nov 4, 2026

REVISION
0 · Issued for pricing

UNITS
Inches. Use written dimensions; do not scale.


STATUS
For quotation. Fabricator submits shop drawings and finish samples for approval before production.

REV · DATE · DESCRIPTION
0 · 11/04/26 · Issued for pricing


SHEET
A-104

3D VIEWS


Isometric views

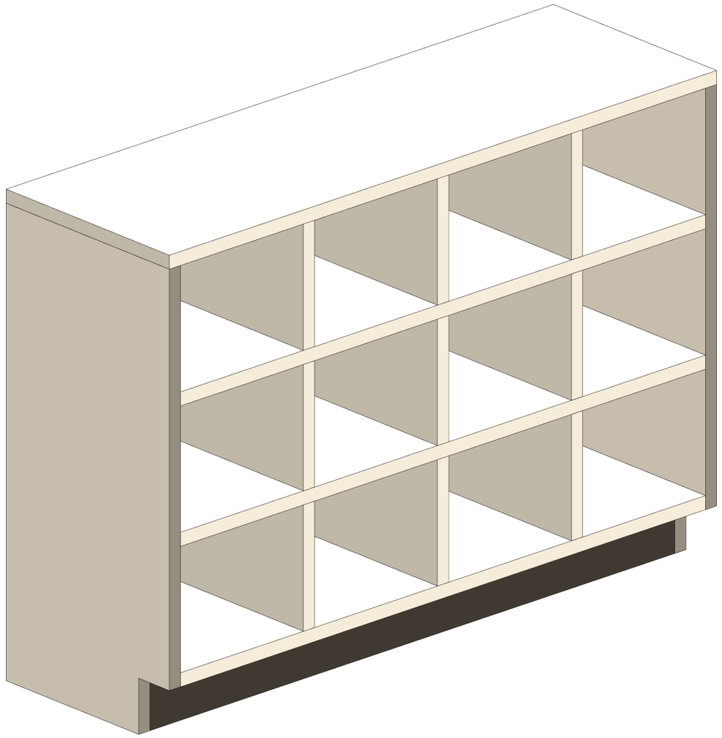


FRONT ISOMETRIC · EMPTY

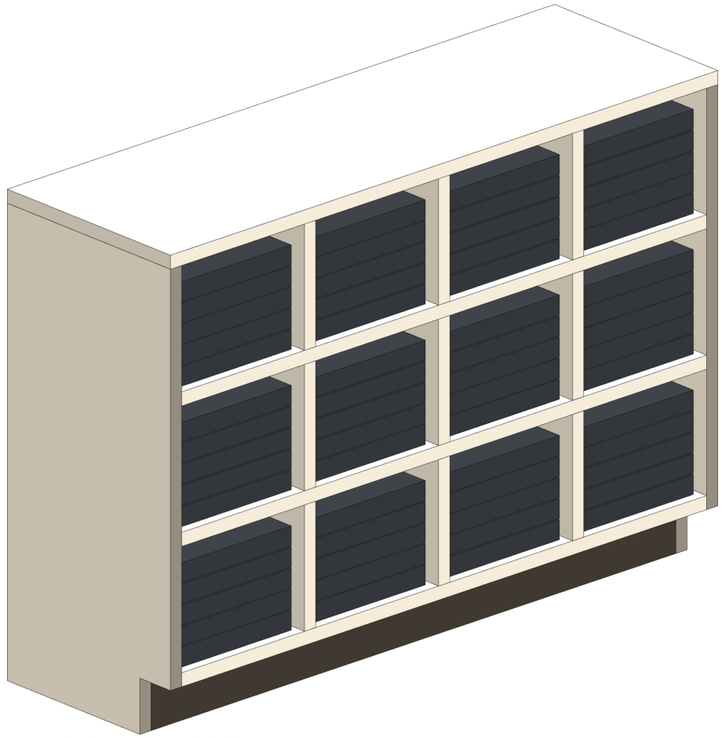

FRONT ISOMETRIC · LOADED, 60 LAPTOPS

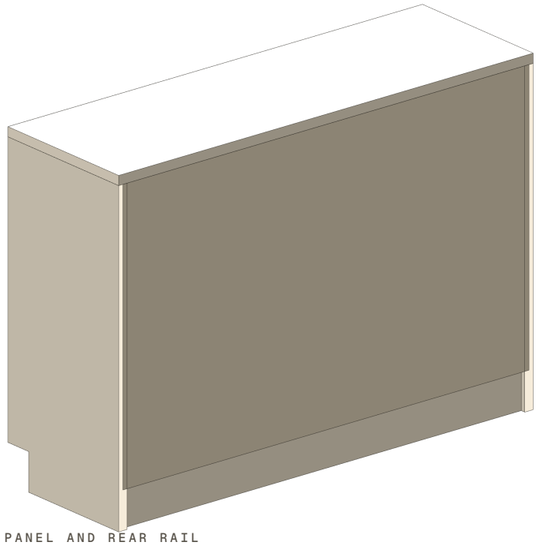

REAR ISOMETRIC · BACK PANEL AND REAR RAIL

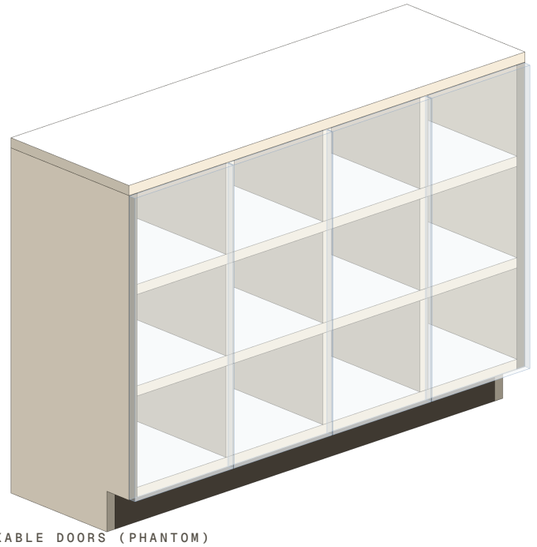

ALTERNATE ALT-1 · LOCKABLE DOORS (PHANTOM)

OF4S

Office Furniture 4 Sale
1790 W 8th Ave, Hialeah, FL 33010
+1 305 889 3364 · officefurniture4sale.com

PROJECT
LC-60 laptop storage cabinet

CLIENT
To be confirmed

DRAWING
Isometric views

SCALE
Not to scale

DATE
Nov 4, 2026

REVISION
0 · Issued for pricing

UNITS
Inches. Use written dimensions; do not scale.


STATUS
For quotation. Fabricator submits shop drawings and finish samples for approval before production.

REV · DATE · DESCRIPTION
0 · 11/04/26 · Issued for pricing

SHEET
A-201

ASSEMBLY

Exploded isometric

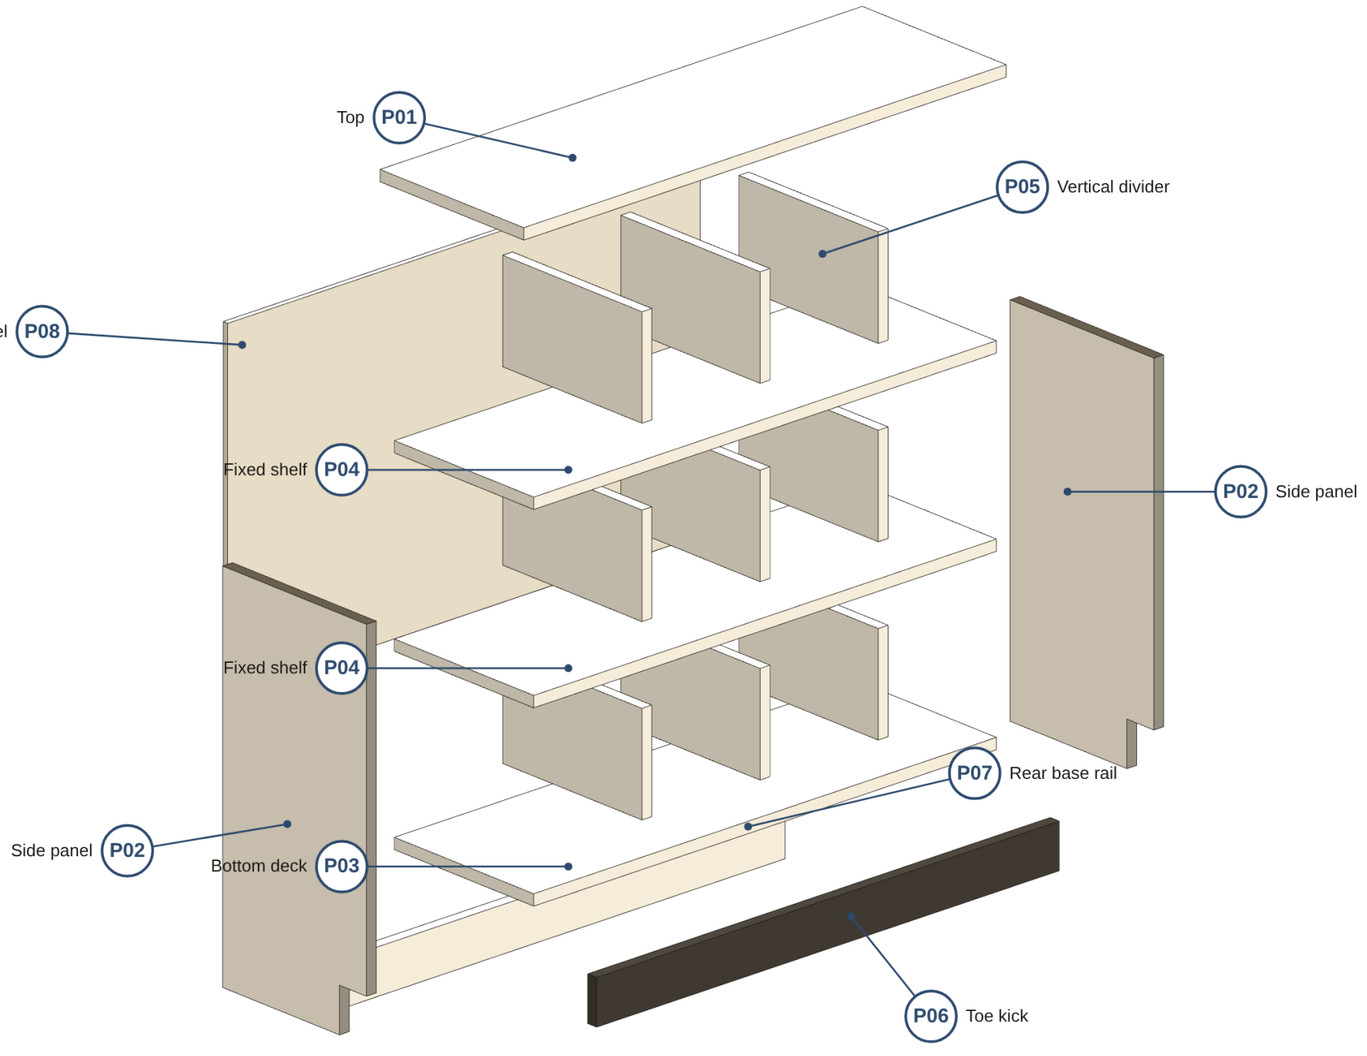

PART LEGEND

P01 **Top**
Qty 1 · 49" x 16" x 1"

P02 **Side panel**
Qty 2 · 34" x 16" x 1"

P03 **Bottom deck**
Qty 1 · 47" x 15-1/2" x 1"

P04 **Fixed shelf**
Qty 2 · 47" x 15-1/2" x 1"

P05 **Vertical divider**
Qty 9 · 9" x 15-1/2" x 1"

P06 **Toe kick**
Qty 1 · 47" x 4" x 1"

P07 **Rear base rail**
Qty 1 · 47" x 4" x 1"

P08 **Back panel**
Qty 1 · 48" x 30" x 1/2"

ASSEMBLY SEQUENCE

1. Band edges; drill per A-301/A-302.
2. Sides to bottom deck, toe kick, rear rail.
3. Tier 1 dividers, then shelf 1.
4. Tier 2 dividers, then shelf 2.
5. Tier 3 dividers, then top.
6. Square up; fit back into rabbets.
7. Glides; anti-tip kit on site.

OF4S

Office Furniture 4 Sale
1790 W 8th Ave, Hialeah, FL 33010
+1 305 889 3364 · officefurniture4sale.com

PROJECT
LC-60 laptop storage cabinet

CLIENT
To be confirmed

DRAWING
Exploded isometric

SCALE
Not to scale

DATE
Nov 4, 2026

REVISION
0 · Issued for pricing

UNITS
Inches. Use written dimensions; do not scale.

STATUS
For quotation. Fabricator submits shop drawings and finish samples for approval before production.

REV · DATE · DESCRIPTION
0 · 11/04/26 · Issued for pricing

SHEET
A-202


PART DETAILS

Top, side, bottom deck, shelf

Edgeband, 3 mm PVC · Mating part location · Hidden


P01 Top

QTY 1 · 1" THICK · 1" TFM BOARD · SCALE 1:8

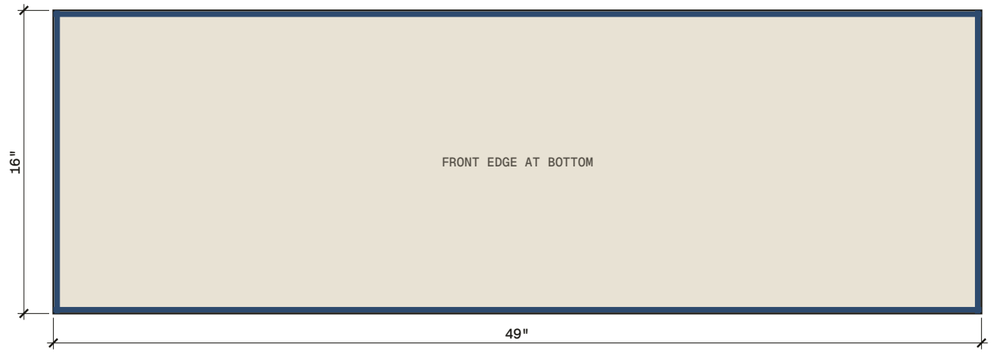


P03 Bottom deck


QTY 1 · 1" THICK · 1" TFM BOARD · SCALE 1:8

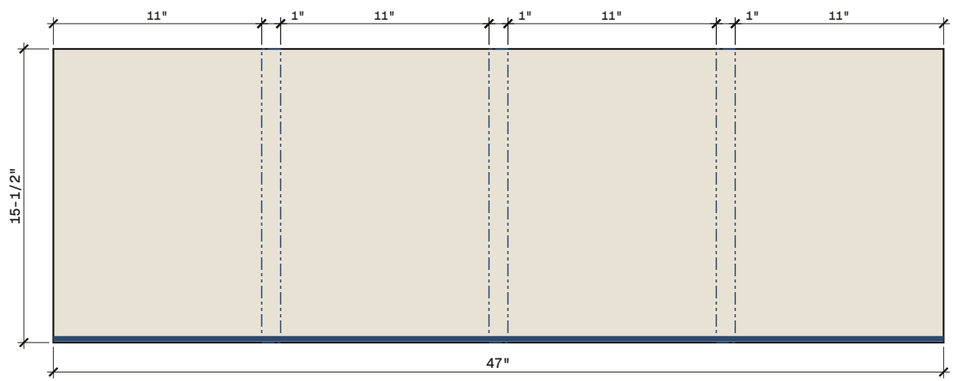

P04 Fixed shelf

QTY 2 · 1" THICK · 1" TFM BOARD · SCALE 1:8

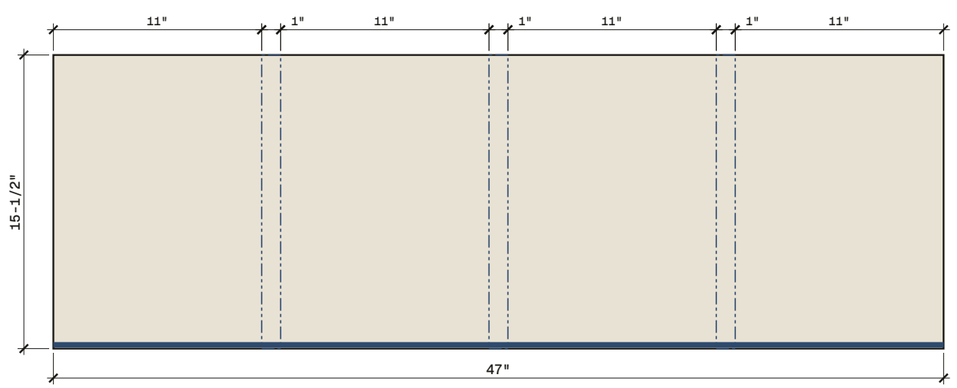

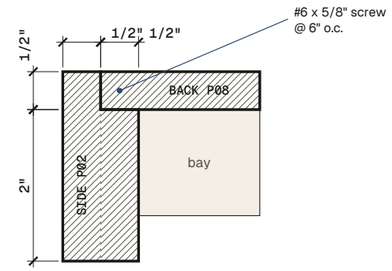


8 Rabbet

PLAN DETAIL, SCALE 1:2

P02 Side panel (left & right, mirror pair)

QTY 2 · 1" THICK · 1" TFM BOARD · SCALE 1:8

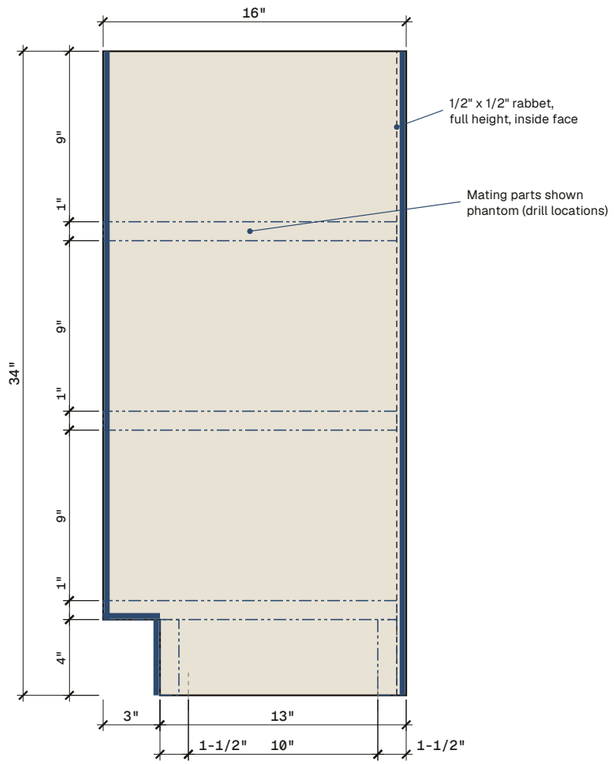

Shown: right side, viewed from outside. Left side is the mirror.

OF4S

Office Furniture 4 Sale
1790 W 8th Ave, Hialeah, FL 33010
+1 305 889 3364 · officefurniture4sale.com

PROJECT
LC-60 laptop storage cabinet

CLIENT
To be confirmed

DRAWING
Part details 1

SCALE
1:8, 1:2 at 11 x 17

DATE
Nov 4, 2026

REVISION
0 · Issued for pricing

UNITS
Inches. Use written dimensions; do not scale.

STATUS
For quotation. Fabricator submits shop drawings and finish samples for approval before production.

REV · DATE · DESCRIPTION
0 · 11/04/26 · Issued for pricing

SHEET
A-301


PART DETAILS

Divider, toe kick, rear rail, back panel

Edgeband, 3 mm PVC · Mating part location · Hidden


P08 Back panel

QTY 1 · 1/2" THICK · 1/2" TFM BACK · SCALE 1:8

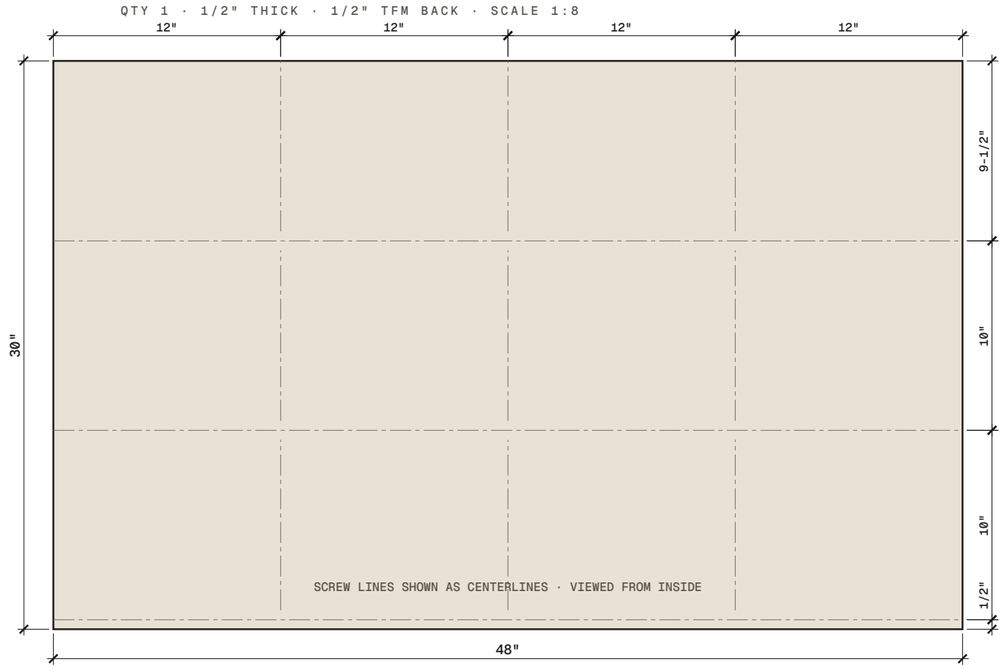


P06 Toe kick

QTY 1 · 1" THICK · 1" TFM BOARD · SCALE 1:8

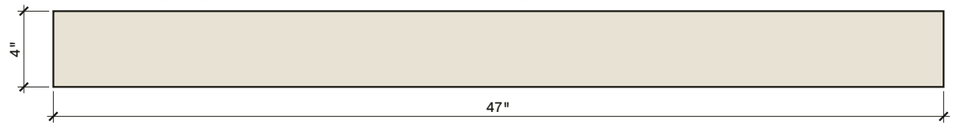


P07 Rear base rail

QTY 1 · 1" THICK · 1" TFM BOARD · SCALE 1:8

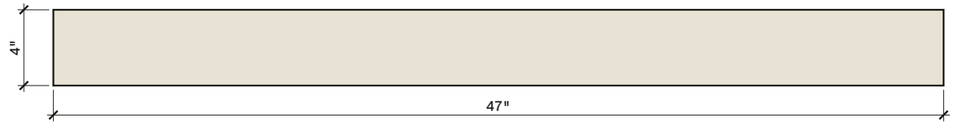

P05 Vertical divider

QTY 9 · 1" THICK · 1" TFM BOARD · SCALE 1:8

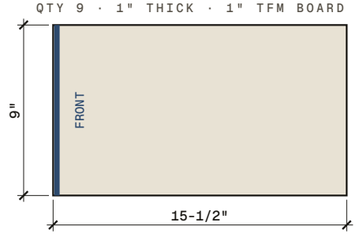

JOINERY AND MACHINING

- Dividers: two 8 mm dowels each end into shelf or deck, glued. Align in one vertical line per column.
- Top, deck, shelves, toe kick and rear rail to sides: dowels plus 7 x 50 mm confirmat screws, 3 per joint (2 at kick and rail). Cap exposed heads.
- Back panel: screwed into rabbets and along the centerlines shown, #6 x 5/8" at 6" o.c.
- Toe kick and rear rail are not edgebanded. Toe kick face in black or dark laminate if available.
- Glides: threaded inserts in side bottom edges at the locations on A-301.
- Tolerances: parts +/- 1/32". Assembled carcass square within 1/16" on diagonals.

OF4S

Office Furniture 4 Sale
1790 W 8th Ave, Hialeah, FL 33010
+1 305 889 3364 · officefurniture4sale.com

PROJECT
LC-60 laptop storage cabinet

CLIENT
To be confirmed

DRAWING
Part details 2

SCALE
1:8 at 11 x 17

DATE
Nov 4, 2026

REVISION
0 · Issued for pricing

UNITS
Inches. Use written dimensions; do not scale.

STATUS
For quotation. Fabricator submits shop drawings and finish samples for approval before production.

REV · DATE · DESCRIPTION
0 · 11/04/26 · Issued for pricing

SHEET
A-302

BILL OF MATERIALS

Cut list, hardware and materials

CUT LIST · FINISHED SIZES, INCLUDING EDGEBAND

MARK	PART	QTY	LENGTH	WIDTH	THK	MATL	EDGEBAND	NOTES	SQ FT
P01	Top	1	49"	16"	1"	M1	All 4 edges	Sits on top of side panels. Flush front, back and ends. Band all 4 edges.	5.4
P02	Side panel (left & right, mirror pair)	2	34"	16"	1"	M1	Front, rear, notch	Toe-kick notch 3" deep x 4" high at front bottom. 1/2" x 1/2" rabbet full height on rear inside edge for back panel. Make one left and one right.	7.6
P03	Bottom deck	1	47"	15-1/2"	1"	M1	Front	Between sides, top surface at 5" AFF. Band front edge.	5.1
P04	Fixed shelf	2	47"	15-1/2"	1"	M1	Front	Fixed (not adjustable). Supported by dividers below every 12". Band front edge.	10.1
P05	Vertical divider	9	9"	15-1/2"	1"	M1	Front	Grain/length vertical. 3 per tier, stacked in line. Band front edge.	8.7
P06	Toe kick	1	47"	4"	1"	M1	None	Between sides, front face recessed 3" (flush with notch).	1.3
P07	Rear base rail	1	47"	4"	1"	M1	None	Between sides under rear of bottom deck, back face flush with back of deck.	1.3
P08	Back panel	1	48"	30"	1/2"	M2	None	Captured in side rabbets, screwed to rear edges of deck, shelves and dividers #6 x 5/8" pan head at 6" o.c.	10.0

HARDWARE

MARK	ITEM	QTY	NOTES
H01	Leveling glide, 5/16"-18, 1-1/4" dia. nylon base, with threaded insert	4	Into bottom edge of each side panel, 2 per side. Adds about 3/8" (see note 6).
H02	8 mm x 35 mm fluted hardwood dowel	60	Divider ends (2 per end) and carcass joints. Glued.
H03	7 x 50 mm confirmat screw (or cam + bolt if shipped knock-down)	36	Sides to top, bottom deck, shelves, toe kick and rear rail. Heads capped.
H04	Confirmat cover cap, color-matched	36	Exposed screw heads on side panels.
H05	#6 x 5/8" pan-head screw	40	Back panel to rabbets and rear edges, 6" o.c.
H06	Anti-tip wall bracket kit (pair) with fasteners	1	Under top at rear. Required: loaded weight about 475 lb.
H07	3 mm PVC, color-matched, radiused 1/16" (≈ 1 mm)	45 LF	See cut list for linear feet.

MATERIAL SUMMARY

CODE	MATERIAL	NET AREA	EST. SHEETS
M1	1" industrial particleboard core, thermally fused laminate (TFM) both faces	39.5 sf	2 @ 49" x 97"
M2	1/2" MDF, TFM both faces (interior face to match carcass)	10.0 sf	1 @ 49" x 97"
EB	3 mm PVC, color-matched, radiused 1/16" (≈ 1 mm)	41.2 LF	45 LF w/ 10%
	Weight, empty / loaded (approx.)	175 lb	475 lb

Sheet counts are a nesting estimate for quoting. Fabricator to optimize. Color: by owner, to be confirmed. Quote standard TFM colors at no upcharge.

OF4S

Office Furniture 4 Sale
1790 W 8th Ave, Hialeah, FL 33010
+1 305 889 3364 · officefurniture4sale.com

PROJECT
LC-60 laptop storage cabinet

CLIENT
To be confirmed

DRAWING
Cut list and hardware

SCALE
None

DATE
Nov 4, 2026

REVISION
0 · Issued for pricing

UNITS
Inches. Use written dimensions; do not scale.


STATUS
For quotation. Fabricator submits shop drawings and finish samples for approval before production.

REV · DATE · DESCRIPTION
0 · 11/04/26 · Issued for pricing

SHEET
A-401

QUOTATION

Alternates and quote request

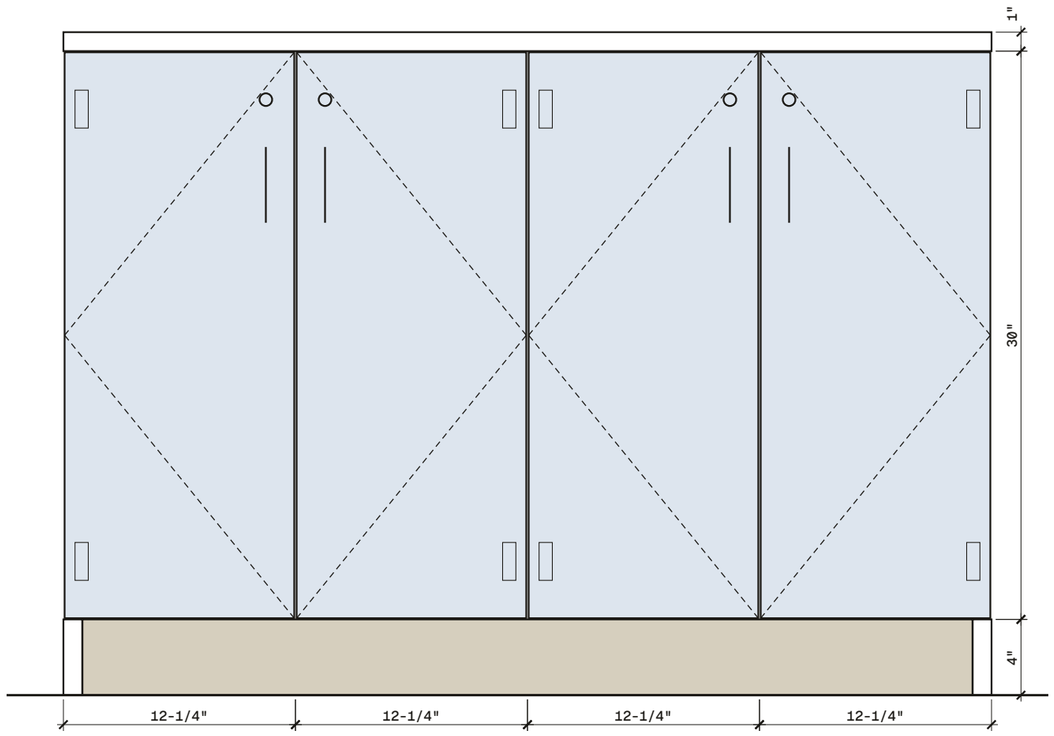

9 ALT-1 lockable doors

FRONT ELEVATION, SCALE 1:8

ALTERNATES · PRICE EACH SEPARATELY, PER CABINET

ALT-1 — Lockable doors
4 full-overlay doors, one per column, 12-1/8" W x 29-7/8" H x 3/4" TFM, 3 mm PVC all edges. 2 concealed 110° soft-close hinges per door (half-overlay on dividers). 1 keyed-alike cam lock per door, 1 wire pull per door (4" c.c.). Adds 3/4" to depth.

ALT-2 — Ventilation
One 2" dia. grommet hole with cap through the back panel at each bay (12), or 3 x 1/2" x 6" routed vent slots per bay. Needed if laptops go in warm.

ALT-3 — Charging
Not in base scope. If laptops must charge inside, quote a UL-listed charging solution separately (power strips inside casework are not code-compliant).

ALT-4 — Mobile base
Replace toe kick and rear rail with a 1" sub-base on 4 x 3" locking casters, keeping 35" overall height.

ALT-5 — Bay labels
Engraved or printed bay ID plates A1 to D3 on shelf fronts, 12 total.

PLEASE QUOTE

1. Unit price for the base cabinet as drawn, at quantities of 1, 2 and 5.
2. Each alternate (ALT-1 to ALT-5) as a separate add per cabinet.
3. Freight to 1790 W 8th Ave, Hialeah, FL 33010, and whether it ships assembled or knock-down.
4. Lead time from shop-drawing approval.
5. Standard laminate colors available at no upcharge, and edgeband match.
6. Warranty terms.
7. Any change you recommend for cost or strength (for example 3/4" dividers). Price it as a voluntary alternate; do not substitute in the base price.

OPEN ITEMS · OWNER TO CONFIRM BEFORE RELEASE

- Exact laptop model and size, with or without a protective case.
- Will laptops charge inside the cabinet? If yes, see ALT-2 and ALT-3.
- Doors and locks required? (ALT-1)
- Is 35" a hard maximum (under a window or counter)? Glides add about 3/8".
- Wall-mounted location, or freestanding with a finished back?
- Laminate color and number of cabinets.

CONTACT

Office Furniture 4 Sale · +1 305 889 3364
officefurniture4sale.com

OF4S

Office Furniture 4 Sale
1790 W 8th Ave, Hialeah, FL 33010
+1 305 889 3364 · officefurniture4sale.com

PROJECT
LC-60 laptop storage cabinet

CLIENT
To be confirmed

DRAWING
Alternates, quote request

SCALE
1:8 at 11 x 17

DATE
Nov 4, 2026

REVISION
0 · Issued for pricing

UNITS
Inches. Use written dimensions; do not scale.

STATUS
For quotation. Fabricator submits shop drawings and finish samples for approval before production.

REV · DATE · DESCRIPTION

REV	DATE	DESCRIPTION
0	11/04/26	Issued for pricing

SHEET
A-501